

1 BÈ PIN 01
1 : 900

SỐ TẤM PIN MẶT TRỜI THEO BÈ		
DẢI PIN	**SỐ LƯỢNG HÀNG**	**Số tấm pin**
DẢI PIN MẶT TRỜI	100	2800
Grand total: 100		2800

SỐ PHAO NỔI THEO BÈ		
DẢI PIN	**SỐ LƯỢNG HÀNG**	SỐ PHAO
DẢI PHAO ĐI LẠI	2	202
DẢI PHAO ĐI LẠI	3	303
DẢI PHAO ĐỠ PIN	104	2912
Grand total: 109		3417

INVESTER		
Thiết bị	**Loại Invester**	**Số lượng**
Invester	SG -510HX	4
Grand total: 4		

SỬA REV.	NGÀY DATE	PHÊ DUYỆT APPRVD. BY	MÔ TẢ DESCRIPTION

N

DỰ ÁN / PROJECT:

CHỦ ĐẦU TƯ / INVESTOR:

TƯ VẤN QLDA & TVGS:

PHÊ DUYỆT/ APPROVED BY: | KÝ/ SIGN:

GIÁM SÁT THI CÔNG

NGƯỜI THỰC HIỆN: | KÝ/ SIGN:

LÊ MINH NHẬT

HỒ SƠ / FILE:

HẠNG MỤC / ITEM:

<None>


TÊN BẢN VẼ / DRAWING TITLE:

CHI TIẾT BÈ PIN 01

TỶ LỆ / SCALE:	NGÀY / DATE:	HIỆU CHỈNH / REV.:
	.../2026	00

SỐ BẢN VẼ / DRAWING NO.:

CT-BE01

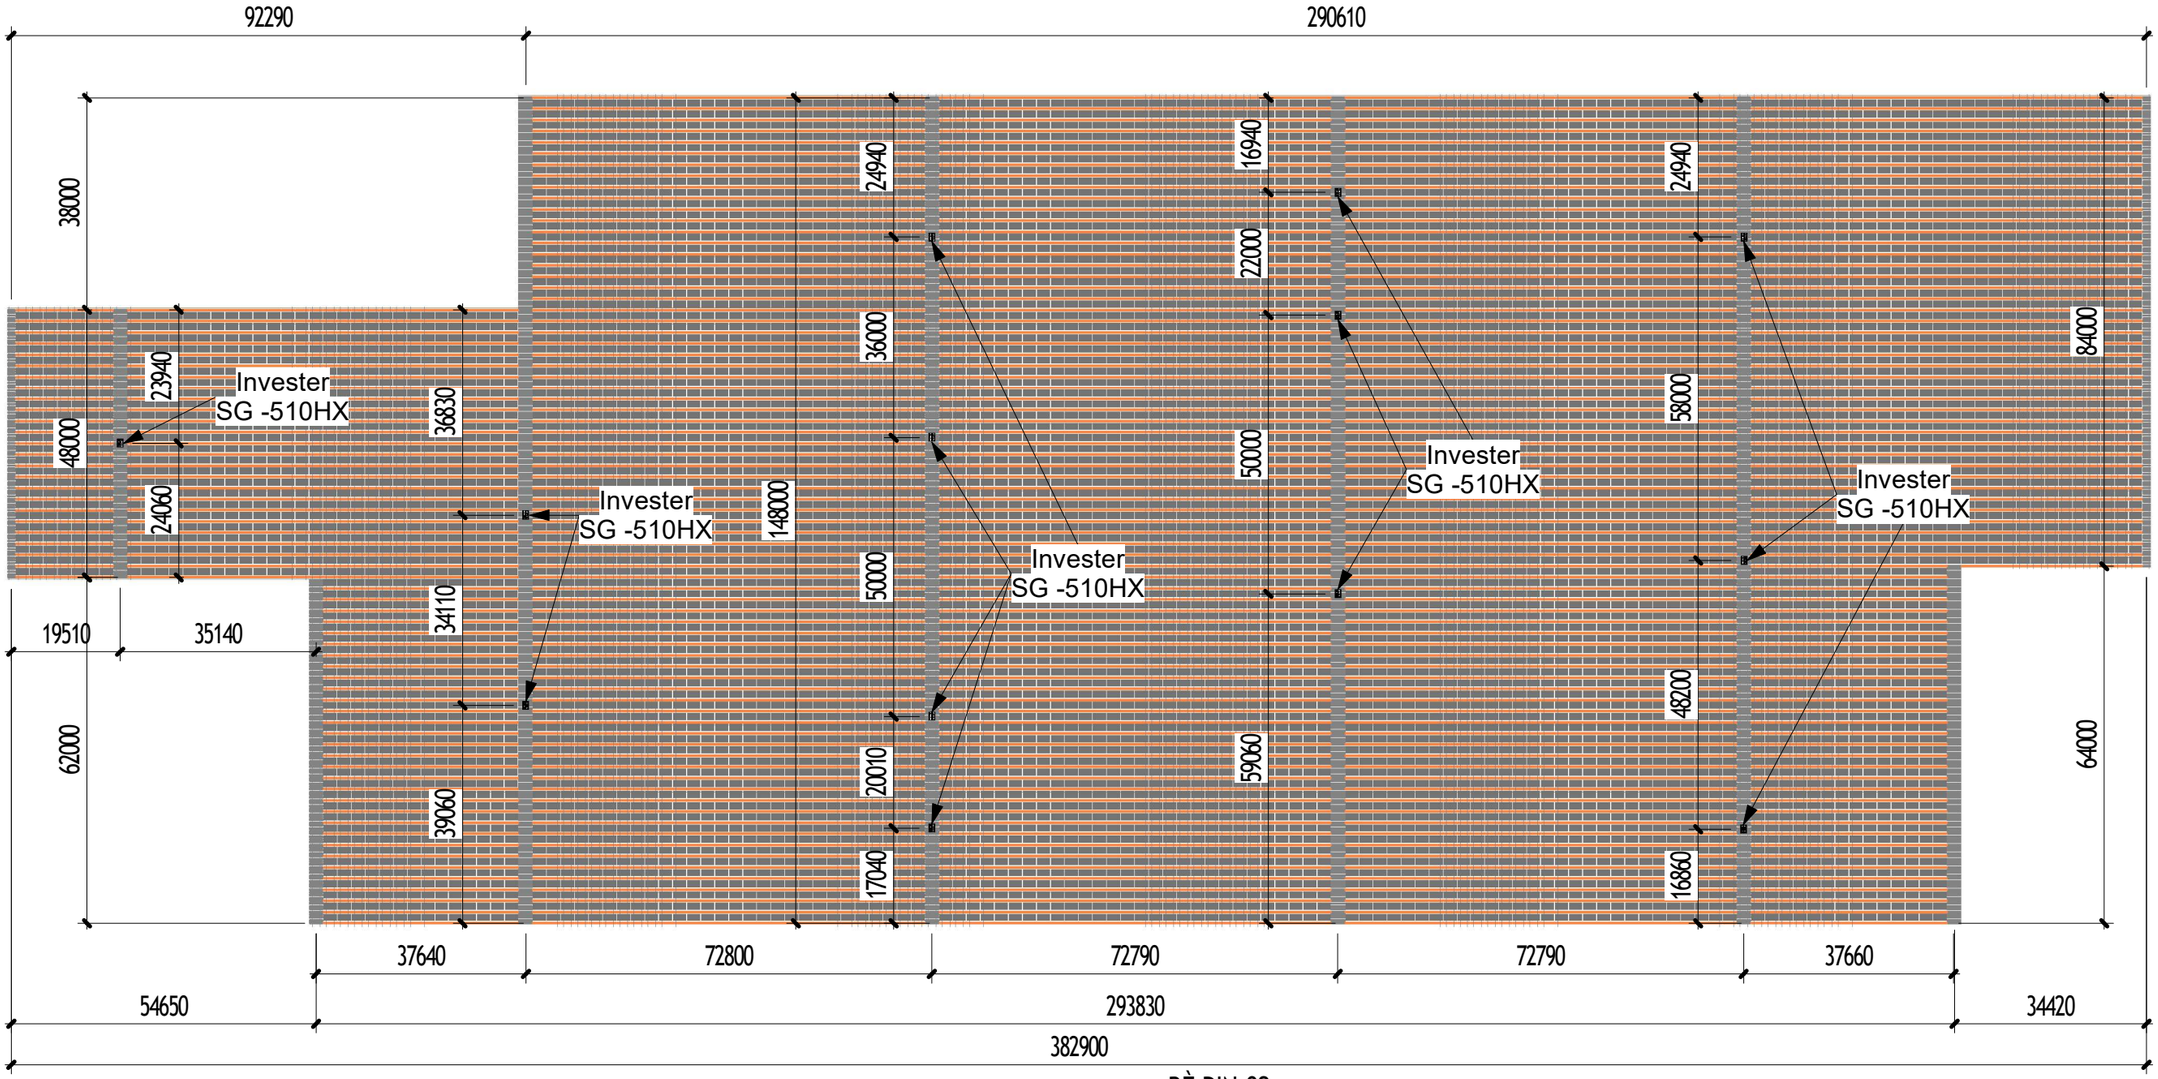

1 BÈ PIN 02
1 : 1100

SỐ TẤM PIN MẶT TRỜI THEO BÈ		
DÃI PIN	SỐ LƯỢNG HÀNG	Số tấm pin
DÃI PIN MẶT TRỜI	375	9114
Grand total: 375		9114

SỐ PHAO NỔI THEO BÈ		
DÃI PIN	SỐ LƯỢNG HÀNG	SỐ PHAO
DÃI PHAO DI LẠI	2	266
DÃI PHAO ĐI LẠI	7	1538
DÃI PHAO ĐỠ PIN	382	9260
Grand total: 391		11064

INVESTER		
Thiết bị	Loại Invester	Số lượng
Invester	SG -510HX	13
Grand total: 13		

SỬA REV.	NGÀY DATE	PHÊ DUYỆT APPRVD. BY	MÔ TẢ DESCRIPTION

N

DỰ ÁN / PROJECT:

CHỦ ĐẦU TƯ / INVESTOR:

TƯ VẤN QLDA & TVGS:

PHÊ DUYỆT/ APPROVED BY: | KÝ/ SIGN:

GIÁM SÁT THI CÔNG

NGƯỜI THỰC HIỆN: LÊ MINH NHẬT | KÝ/ SIGN:


HỒ SƠ / FILE:

HẠNG MỤC / ITEM: <None>

TÊN BẢN VẼ / DRAWING TITLE: CHI TIẾT BÈ PIN 02

TỶ LỆ / SCALE:	NGÀY / DATE:	HIỆU CHỈNH / REV.:
	.../2026	00

SỐ BẢN VẼ / DRAWING NO.: CT-BE02

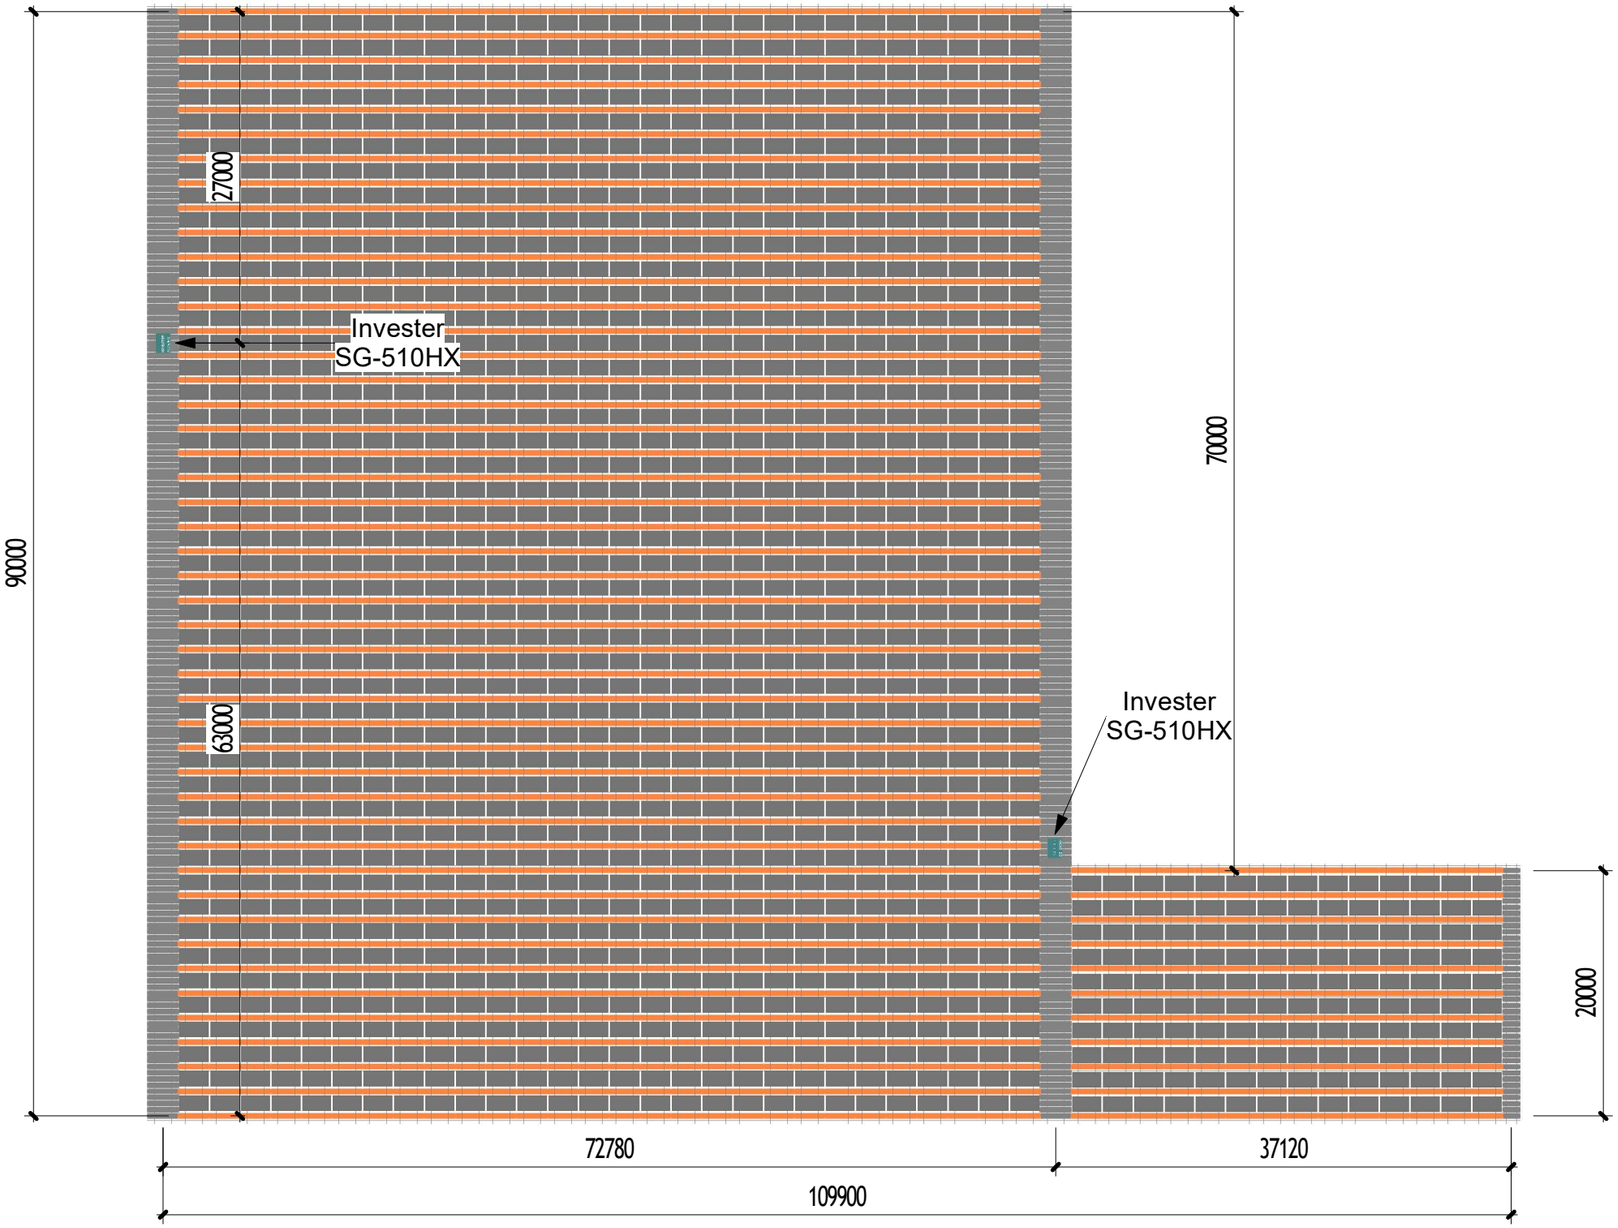

1 BÈ PIN 03
1 : 500

SỐ PHAO NỔI THEO BÈ		
DẢI PIN	SỐ LƯỢNG HÀNG	SỐ PHAO
DẢI PHAO DI LẠI	1	41
DẢI PHAO ĐI LẠI	2	362
DẢI PHAO ĐỠ PIN	57	1442
Grand total: 60		1845

SỐ TẤM PIN MẶT TRỜI THEO BÈ		
DẢI PIN	SỐ LƯỢNG HÀNG	Số tấm pin
DẢI PIN MẶT TRỜI	55	1400
Grand total: 55		1400

INVESTER		
Thiết bị	Loại Invester	Số lượng
Invester	SG-510HX	2
Grand total: 2		

SỬA REV.	NGÀY DATE	PHÊ DUYỆT APPRVD. BY	MÔ TẢ DESCRIPTION

N

DỰ ÁN / PROJECT:

CHỦ ĐẦU TƯ / INVESTOR:

TƯ VẤN QLDA & TVGS:

PHÊ DUYỆT/ APPROVED BY: | KÝ/ SIGN:

GIÁM SÁT THI CÔNG

NGƯỜI THỰC HIỆN: LÊ MINH NHẬT | KÝ/ SIGN:


HỒ SƠ / FILE:

HẠNG MỤC / ITEM: <None>

TÊN BẢN VẼ / DRAWING TITLE: CHI TIẾT BÈ PIN 03

TỶ LỆ / SCALE:	NGÀY / DATE:	HIỆU CHỈNH / REV.:
	.../2026	00

SỐ BẢN VẼ / DRAWING NO.: CT-BE03

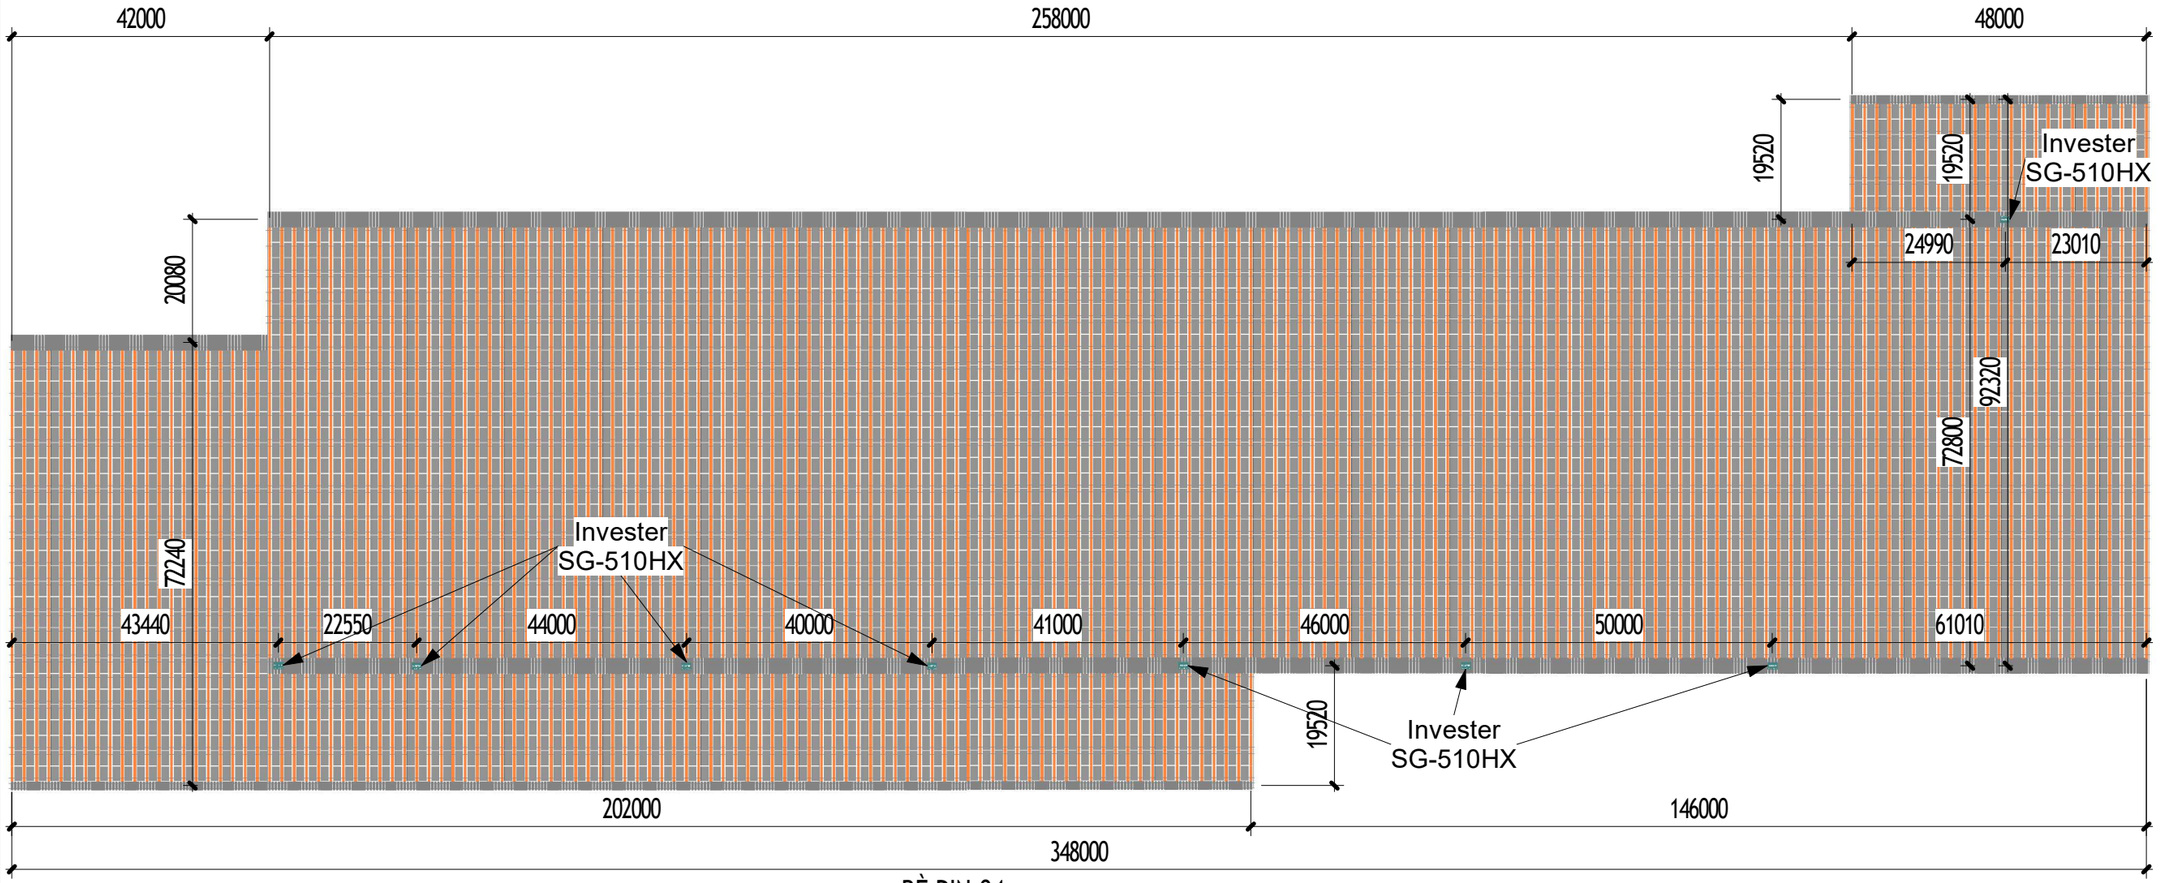

① BÈ PIN 04
1 : 1000

SỐ TẤM PIN MẶT TRỜI THEO BÈ		
DÃI PIN	SỐ LƯỢNG HÀNG	Số tấm pin
DÃI PIN MẶT TRỜI	278	5600
Grand total: 278		5600

SỐ PHAO NỔI THEO BÈ		
DÃI PIN	SỐ LƯỢNG HÀNG	SỐ PHAO
DÃI PHAO DI LẠI	2	502
DÃI PHAO ĐI LẠI	3	1310
DÃI PHAO ĐỠ PIN	281	5642
Grand total: 286		7454

INVESTER		
Thiết bị	Loại Invester	Số lượng
Invester	SG-510HX	8
Grand total: 8		

SỬA REV.	NGÀY DATE	PHÊ DUYỆT APPRVD. BY	MÔ TẢ DESCRIPTION

N

DỰ ÁN / PROJECT:

CHỦ ĐẦU TƯ / INVESTOR:

TƯ VẤN QLDA & TVGS:

PHÊ DUYỆT/ APPROVED BY: | KÝ/ SIGN:

GIÁM SÁT THI CÔNG

NGƯỜI THỰC HIỆN: LÊ MINH NHẬT | KÝ/ SIGN:


HỒ SƠ / FILE:

HẠNG MỤC / ITEM: <None>

TÊN BẢN VẼ / DRAWING TITLE: CHI TIẾT BÈ PIN 04

TỶ LỆ / SCALE:	NGÀY / DATE:	HIỆU CHỈNH / REV.:
	.../2026	00

SỐ BẢN VẼ / DRAWING NO.: CT-BE-04

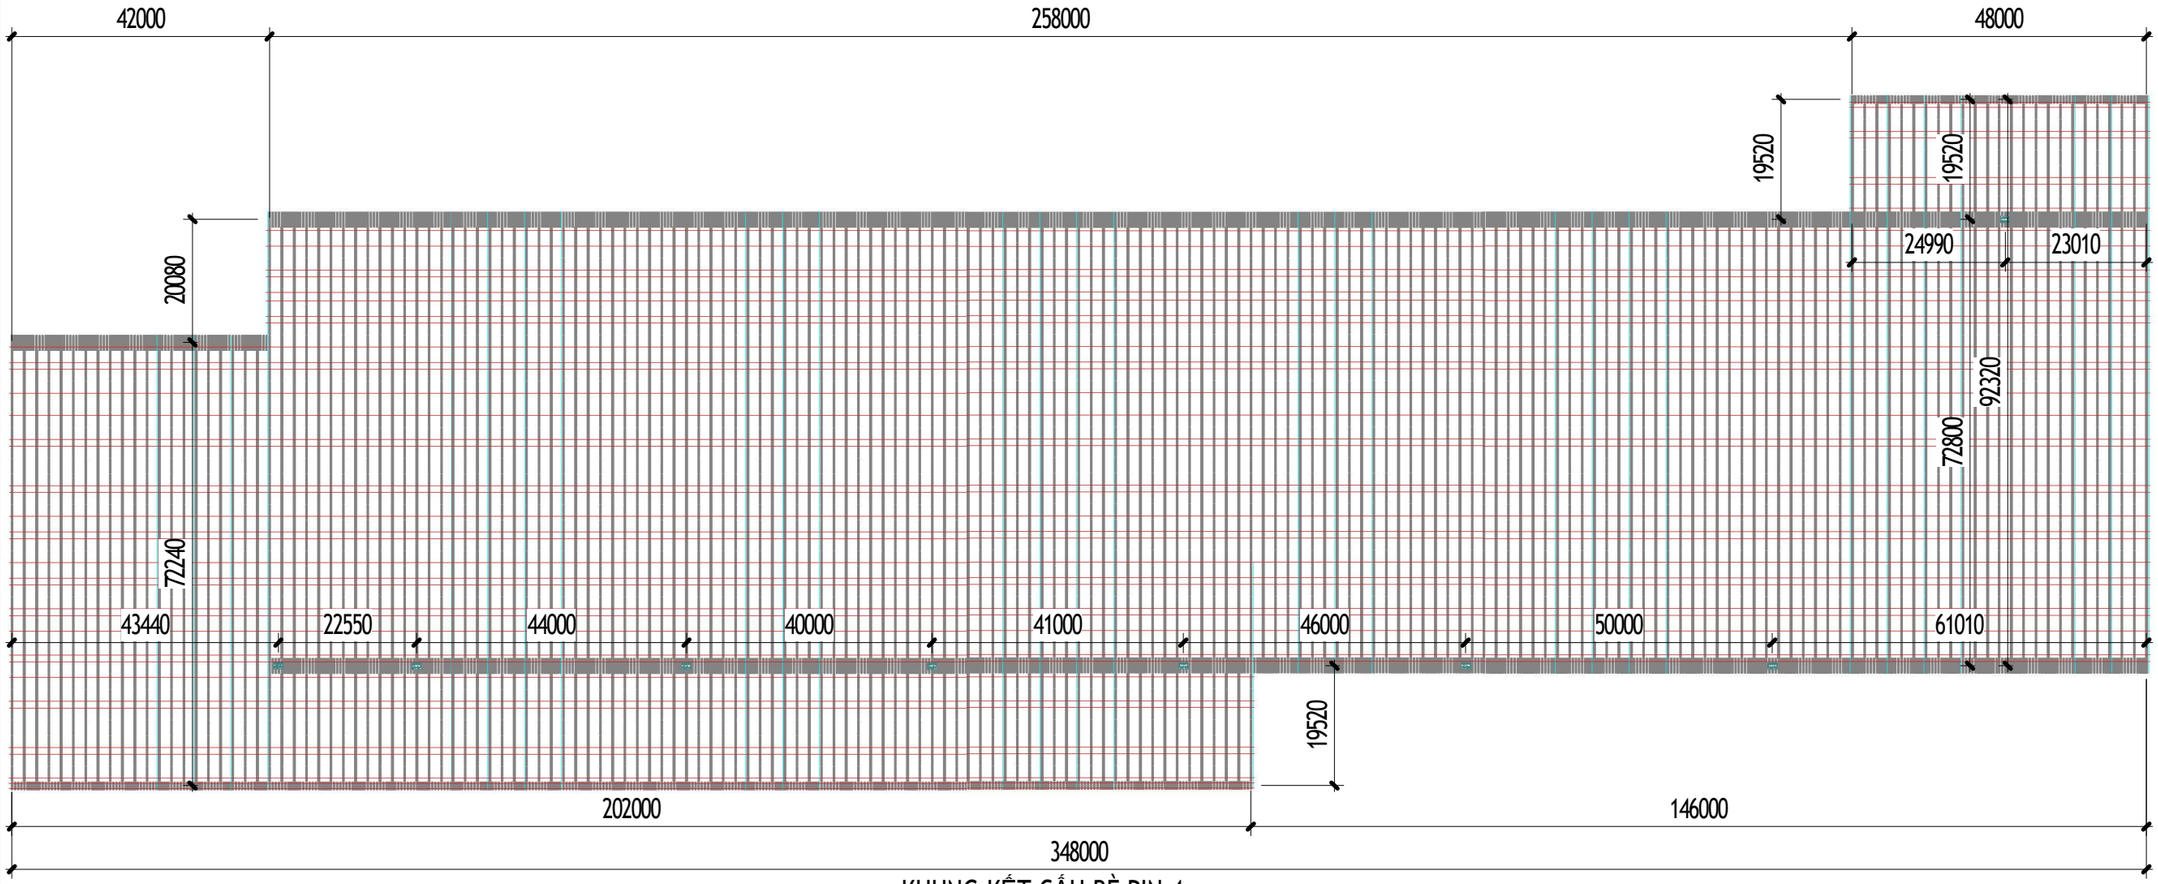

1 KHUNG KẾT CẤU BÈ PIN 4

1 : 1000

THỐNG KÊ KHUNG THÉP

LOẠI	GHI CHÚ	SỐ LƯỢNG	CHIỀU DÀI (m)
Dầm C52		92	24310.61
Hộp 40x60		60	5161.46
Grand total: 152		152	29472.07

SỬA REV.	NGÀY DATE	PHÊ DUYỆT APPRVD. BY	MÔ TẢ DESCRIPTION

N

DỰ ÁN / PROJECT:

CHỦ ĐẦU TƯ / INVESTOR:

TƯ VẤN QLDA & TVGS:

PHÊ DUYỆT/ APPROVED BY: | KÝ/ SIGN:

GIÁM SÁT THI CÔNG

NGƯỜI THỰC HIỆN: LÊ MINH NHẬT | KÝ/ SIGN:

HỒ SƠ / FILE:

HẠNG MỤC / ITEM:

<None>


TÊN BẢN VẼ / DRAWING TITLE:

KHUNG KẾT CẤU BÈ PIN 4

TỶ LỆ / SCALE:	NGÀY / DATE:	HIỆU CHỈNH / REV.:
	.../2026	00

SỐ BẢN VẼ / DRAWING NO.:

KC-BE-04

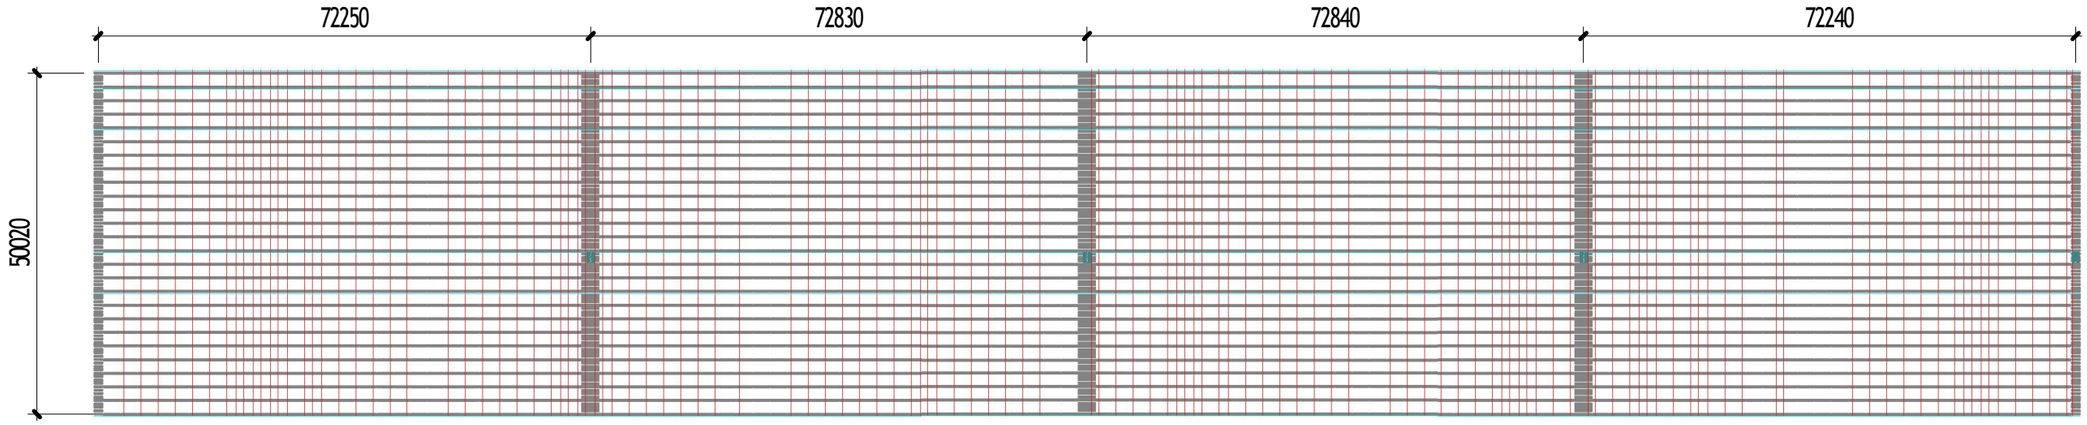

1 KHUNG KẾT CẤU BÈ PIN 1

1 : 900

THỐNG KÊ KHUNG THÉP

LOẠI	GHI CHÚ	SỐ LƯỢNG	CHIỀU DÀI (m)
Dầm C52		234	11925.06
Hộp 40x60		10	2916.22
Grand total: 244		244	14841.28

SỬA REV.	NGÀY DATE	PHÊ DUYỆT APPRVD. BY	MÔ TẢ DESCRIPTION

N

DỰ ÁN / PROJECT:

CHỦ ĐẦU TƯ / INVESTOR:

TƯ VẤN QLDA & TVGS:

PHÊ DUYỆT/ APPROVED BY: | KÝ/ SIGN:

GIÁM SÁT THI CÔNG

NGƯỜI THỰC HIỆN: | KÝ/ SIGN:

LÊ MINH NHẬT

HỒ SƠ / FILE:

HẠNG MỤC / ITEM:

<None>


TÊN BẢN VẼ / DRAWING TITLE:

KHUNG KẾT CẤU BÈ PIN 1

TỶ LỆ / SCALE:	NGÀY / DATE:	HIỆU CHỈNH / REV.:
	.../2026	00

SỐ BẢN VẼ / DRAWING NO.:

KC-BE-01

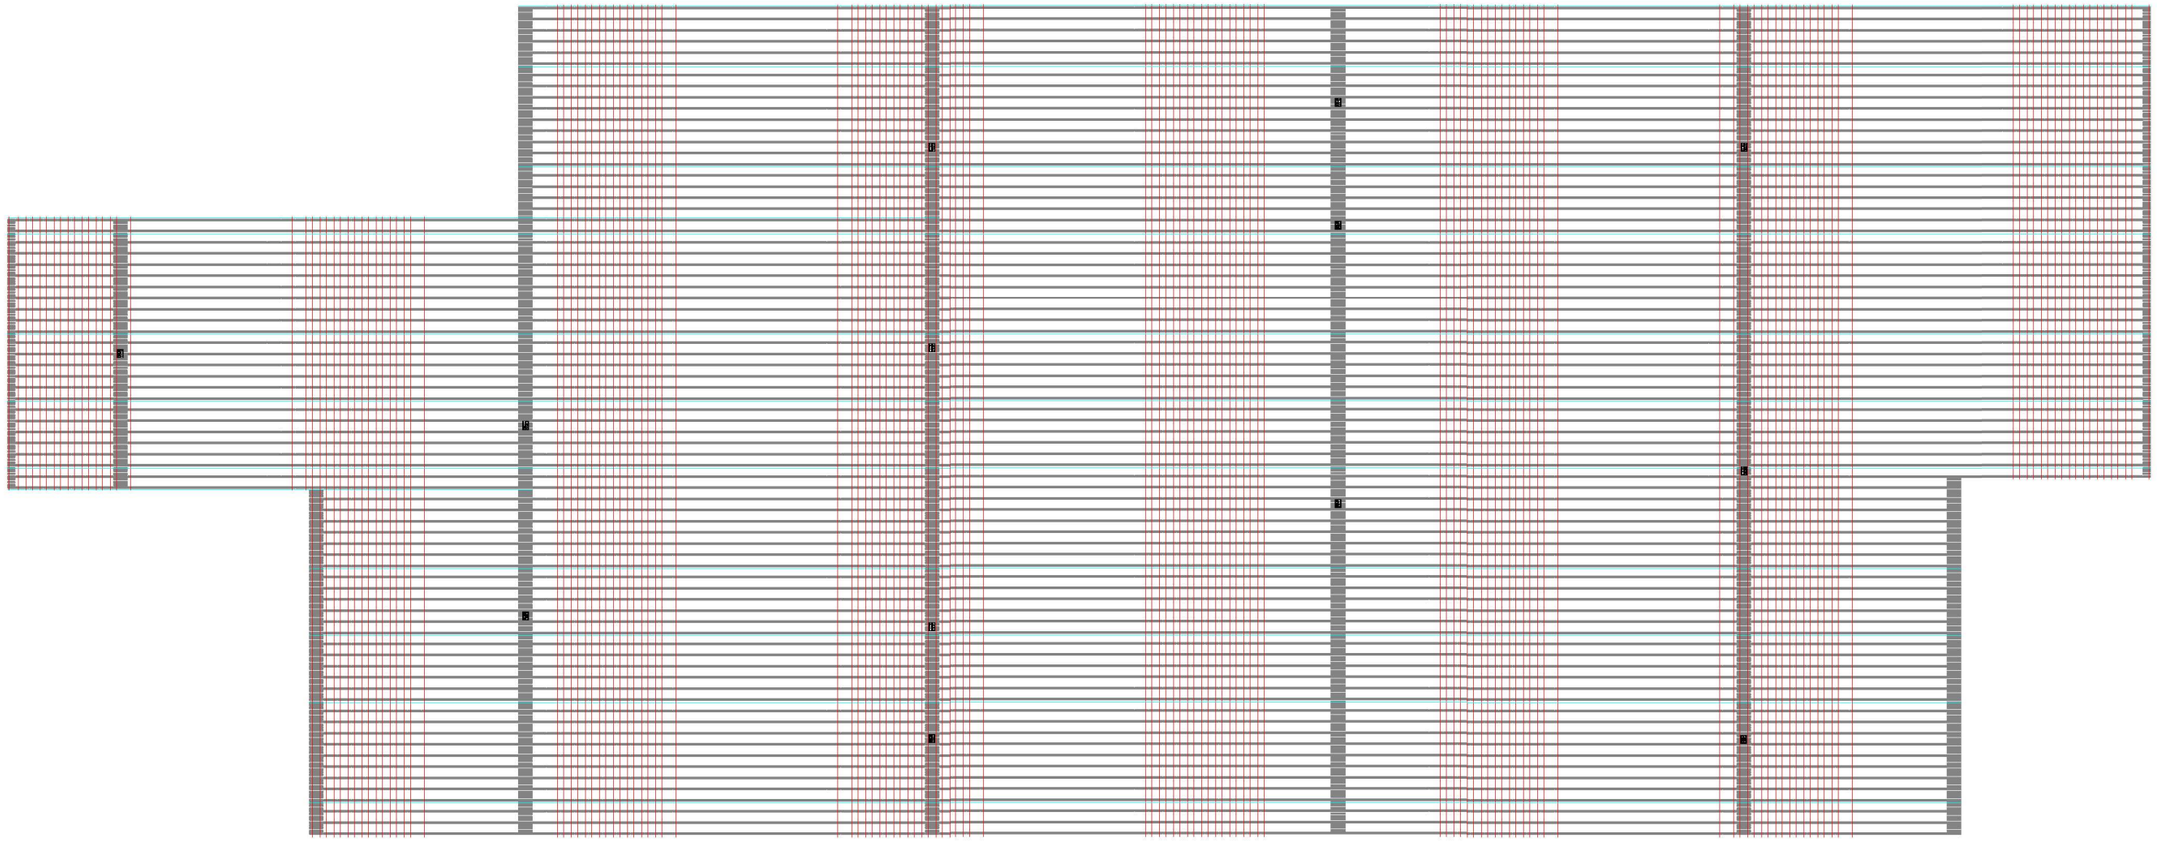

1 KHUNG KẾT CẤU BÈ PIN 2
1 : 1100

THỐNG KÊ KHUNG THÉP

LOẠI	GHI CHÚ	SỐ LƯỢNG	CHIỀU DÀI (m)
Dầm C52		309	38745.81
Hộp 40x60		29	8718.94
Grand total: 338		338	47464.75

SỬA REV.	NGÀY DATE	PHÊ DUYỆT APPRVD. BY	MÔ TẢ DESCRIPTION

N

DỰ ÁN / PROJECT:

CHỦ ĐẦU TƯ / INVESTOR:

TƯ VẤN QLDA & TVGS:

PHÊ DUYỆT/ APPROVED BY: | KÝ/ SIGN:

GIÁM SÁT THI CÔNG

NGƯỜI THỰC HIỆN: | KÝ/ SIGN:

LÊ MINH NHẬT

HỒ SƠ / FILE:

HẠNG MỤC / ITEM:

<None>


TÊN BẢN VẼ / DRAWING TITLE:

KHUNG KẾT CẤU BÈ PIN 2

TỶ LỆ / SCALE:	NGÀY / DATE:	HIỆU CHỈNH / REV.:
	.../2026	00

SỐ BẢN VẼ / DRAWING NO.:

KC-BE-02

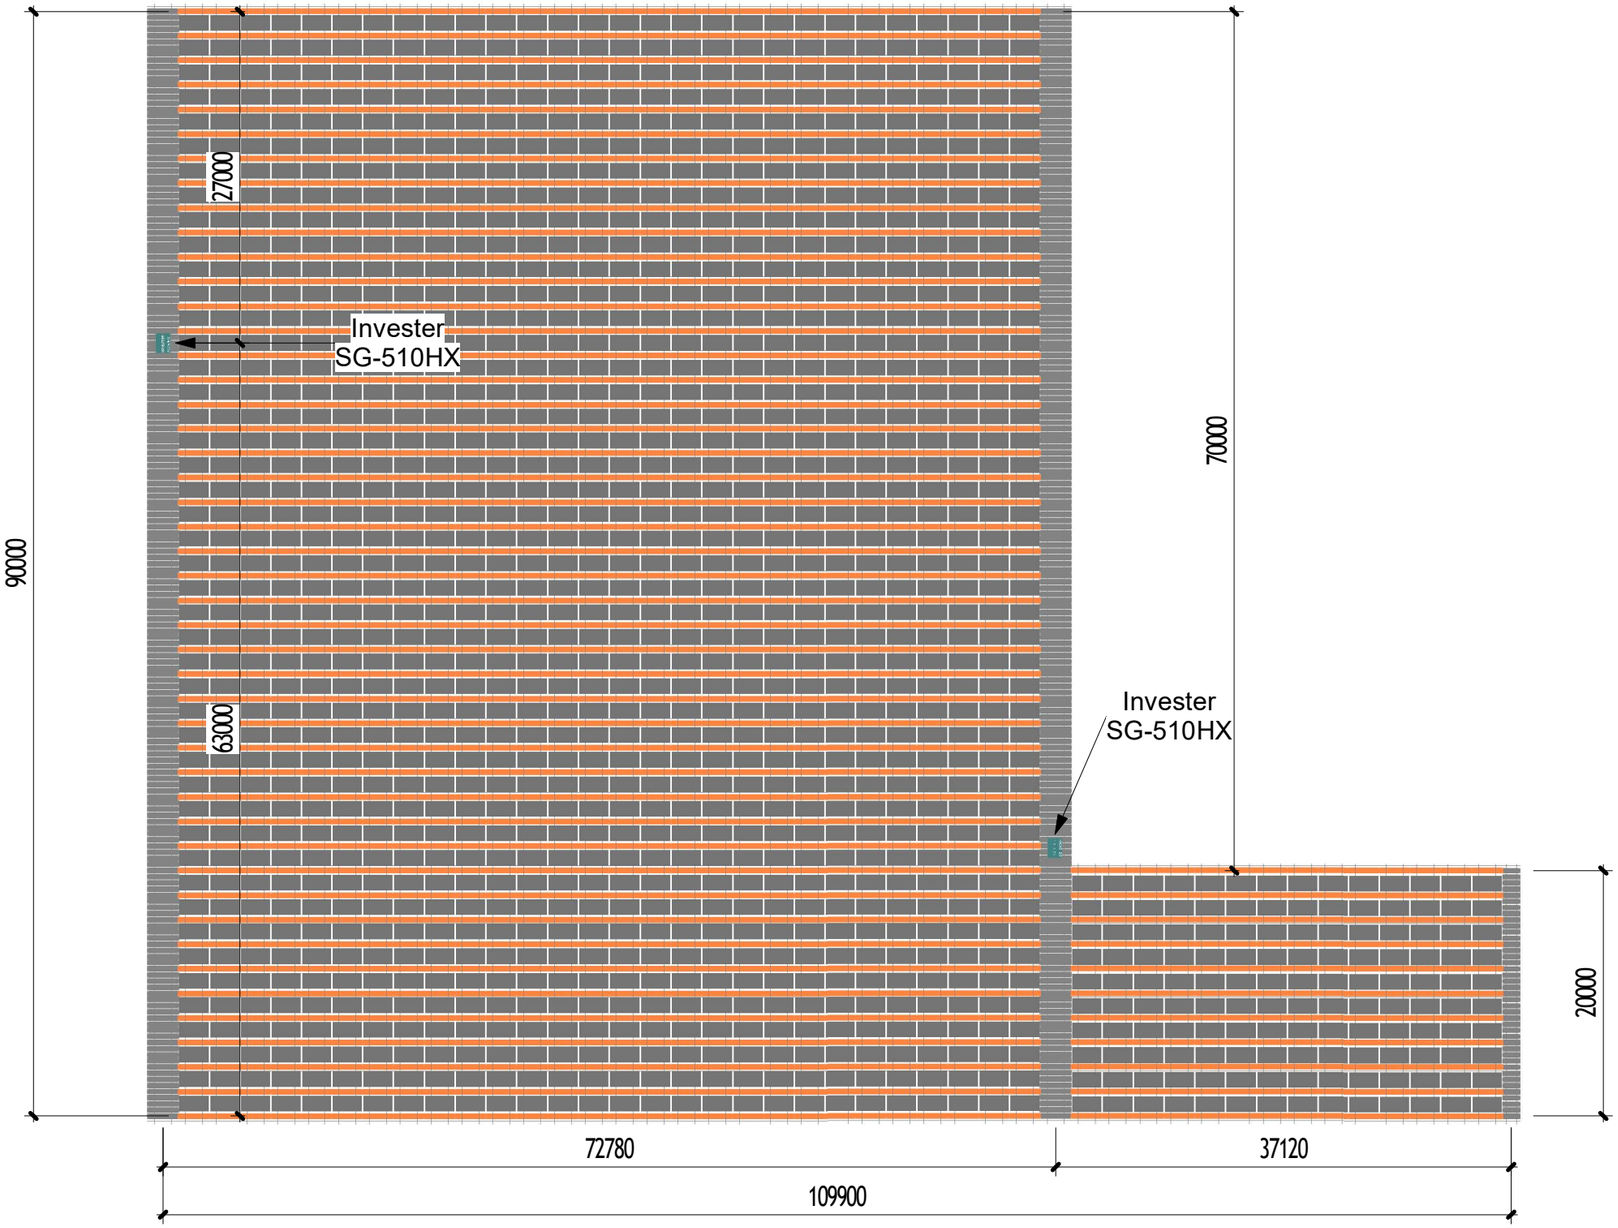

1 3KHUNG KẾT CẤU BỀ PIN 3
1 : 500

THỐNG KÊ KHUNG THÉP

LOẠI	GHI CHÚ	SỐ LƯỢNG	CHIỀU DÀI (m)
Dầm C52		90	6109.92
Hộp 40x60		23	3402.96
Grand total: 113		113	9512.88

SỬA REV.	NGÀY DATE	PHÊ DUYỆT APPRVD. BY	MÔ TẢ DESCRIPTION

N

DỰ ÁN / PROJECT:

CHỦ ĐẦU TƯ / INVESTOR:

TƯ VẤN QLDA & TVGS:

PHÊ DUYỆT/ APPROVED BY: | KÝ/ SIGN:

GIÁM SÁT THI CÔNG

NGƯỜI THỰC HIỆN: | KÝ/ SIGN:

LÊ MINH NHẬT

HỒ SƠ / FILE:

HẠNG MỤC / ITEM:

<None>

TÊN BẢN VẼ / DRAWING TITLE:

KHUNG KẾT CẤU BỀ PIN 3

TỶ LỆ / SCALE:	NGÀY / DATE:	HIỆU CHỈNH / REV.:
	.../2026	00

SỐ BẢN VẼ / DRAWING NO.:

KC-BE-03

PHAO ĐỠ CÁP		
DÃI PIN	**SỐ LƯỢNG HÀNG**	SỐ PHAO
ĐỠ CÁP	1209	2418
Grand total: 1209		2418



1 BỐ TRÍ BÈ PIN MẶT TRỜI
1 : 3000

SỬA REV.	NGÀY DATE	PHÊ DUYỆT APPRVD. BY	MÔ TẢ DESCRIPTION

N

DỰ ÁN / PROJECT:

CHỦ ĐẦU TƯ / INVESTOR:

TƯ VẤN QLDA & TVGS:

PHÊ DUYỆT/ APPROVED BY: | KÝ/ SIGN:

GIÁM SÁT THI CÔNG

NGƯỜI THỰC HIỆN: LÊ MINH NHẬT | KÝ/ SIGN:

HỒ SƠ / FILE:

HẠNG MỤC / ITEM: <None>

TÊN BẢN VẼ / DRAWING TITLE: BỐ TRÍ BÈ PIN MẶT TRỜI

TỶ LỆ / SCALE:	NGÀY / DATE:	HIỆU CHỈNH / REV.:
	.../2026	00

SỐ BẢN VẼ / DRAWING NO.: MB-BP-01