


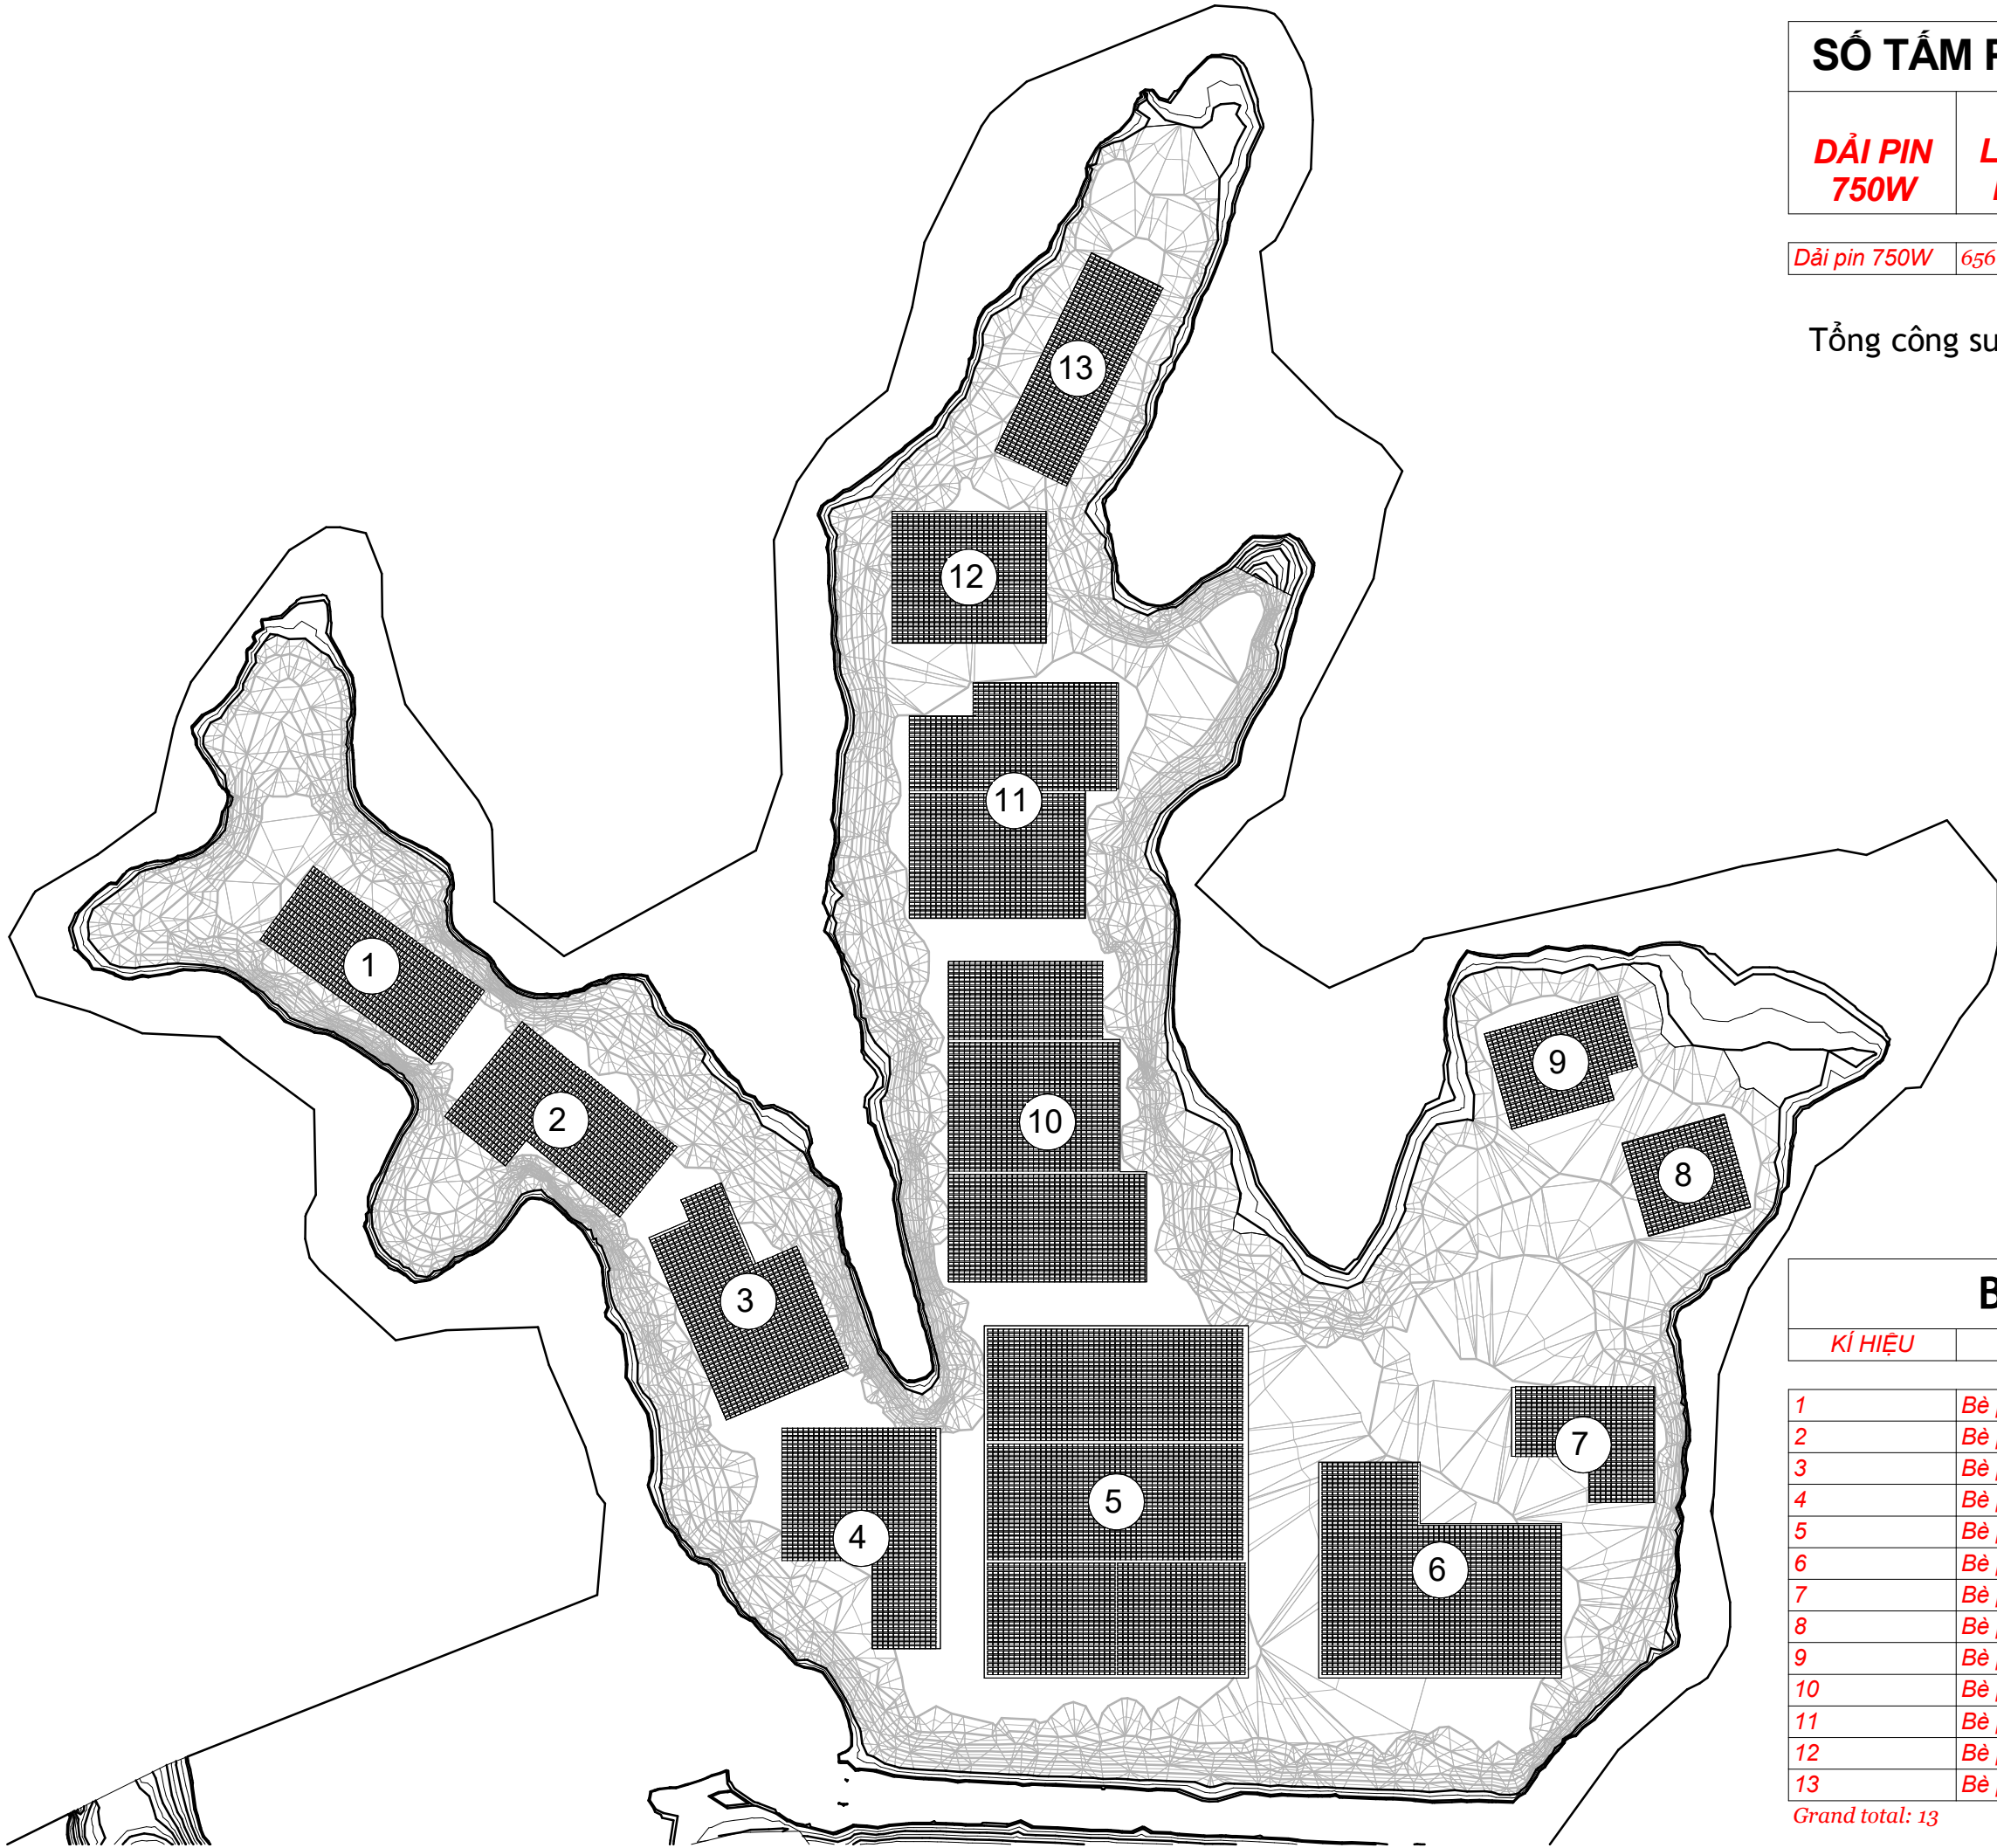

SỐ TẤM PIN MẶT TRỜI		
DÀI PIN 750W	SỐ LƯỢNG HÀNG	Số tấm pin
Dài pin 750W	656	17620

Tổng công suất: 13,2 MWp

BÈ PIN		
KÍ HIỆU	Loại	DIỆN TÍCH
1	Bè pin	3800 m ²
2	Bè pin	4125 m ²
3	Bè pin	4998 m ²
4	Bè pin	5560 m ²
5	Bè pin	19200 m ²
6	Bè pin	9031 m ²
7	Bè pin	2671 m ²
8	Bè pin	2118 m ²
9	Bè pin	2646 m ²
10	Bè pin	11630 m ²
11	Bè pin	8830 m ²
12	Bè pin	4200 m ²
13	Bè pin	3500 m ²
Grand total: 13		82309 m ²

SỬA REV.	NGÀY DATE	PHÉ DUYỆT APPRVD. BY	MÔ TẢ DESCRIPTION
DỰ ÁN / PROJECT:			
CHỦ ĐẦU TƯ / INVESTOR:			
TƯ VẤN QLD&A & TVGS:			
PHÉ DUYỆT/ APPROVED BY:		KÝ/ SIGN:	
GIÁM SÁT THI CÔNG			
NGƯỜI THỰC HIỆN:		KÝ/ SIGN:	
LÊ MINH NHẬT			
HỒ SƠ / FILE:			
HẠNG MỤC / ITEM:			
<None>			
TÊN BẢN VẼ / DRAWING TITLE:			
Bố trí bè pin Hồ Huỗi Vành			
TỶ LỆ / SCALE:	NGÀY / DATE:	HIỆU CHỈNH / REV.:	
	.../2026	00	
SỐ BẢN VẼ / DRAWING NO.:			
MB-B01			