THỐNG KÊ TẤM PIN MẶT TRỜI

Cấu kiện	SỐ LƯỢNG HÀNG	Số tấm pin	Comments	So string
DÃI PIN MẶT TRỜI	84	2352	be 1	84
Grand total: 84		2352		84

THỐNG KÊ KHUNG THÉP

LOẠI	GHI CHÚ	SỐ LƯỢNG	CHIỀU DÀI
Dầm C52		118	10103.04
Hộp 40x60		21	2278.28
Grand total: 139		139	12381.33

SỐ PHAO NỔI THEO BÈ

DÃI PIN	SỐ LƯỢNG HÀNG	SỐ PHAO
DÃI PHAO ĐI LẠI	2	338
DÃI PHAO ĐI LẠI	1	233
DÃI PHAO ĐỠ PIN	86	2408
Grand total: 89		2979

INVESTER

Thiết bị	Loại Invester	Số lượng
Invester	SG -510HX	3
Grand total: 3		

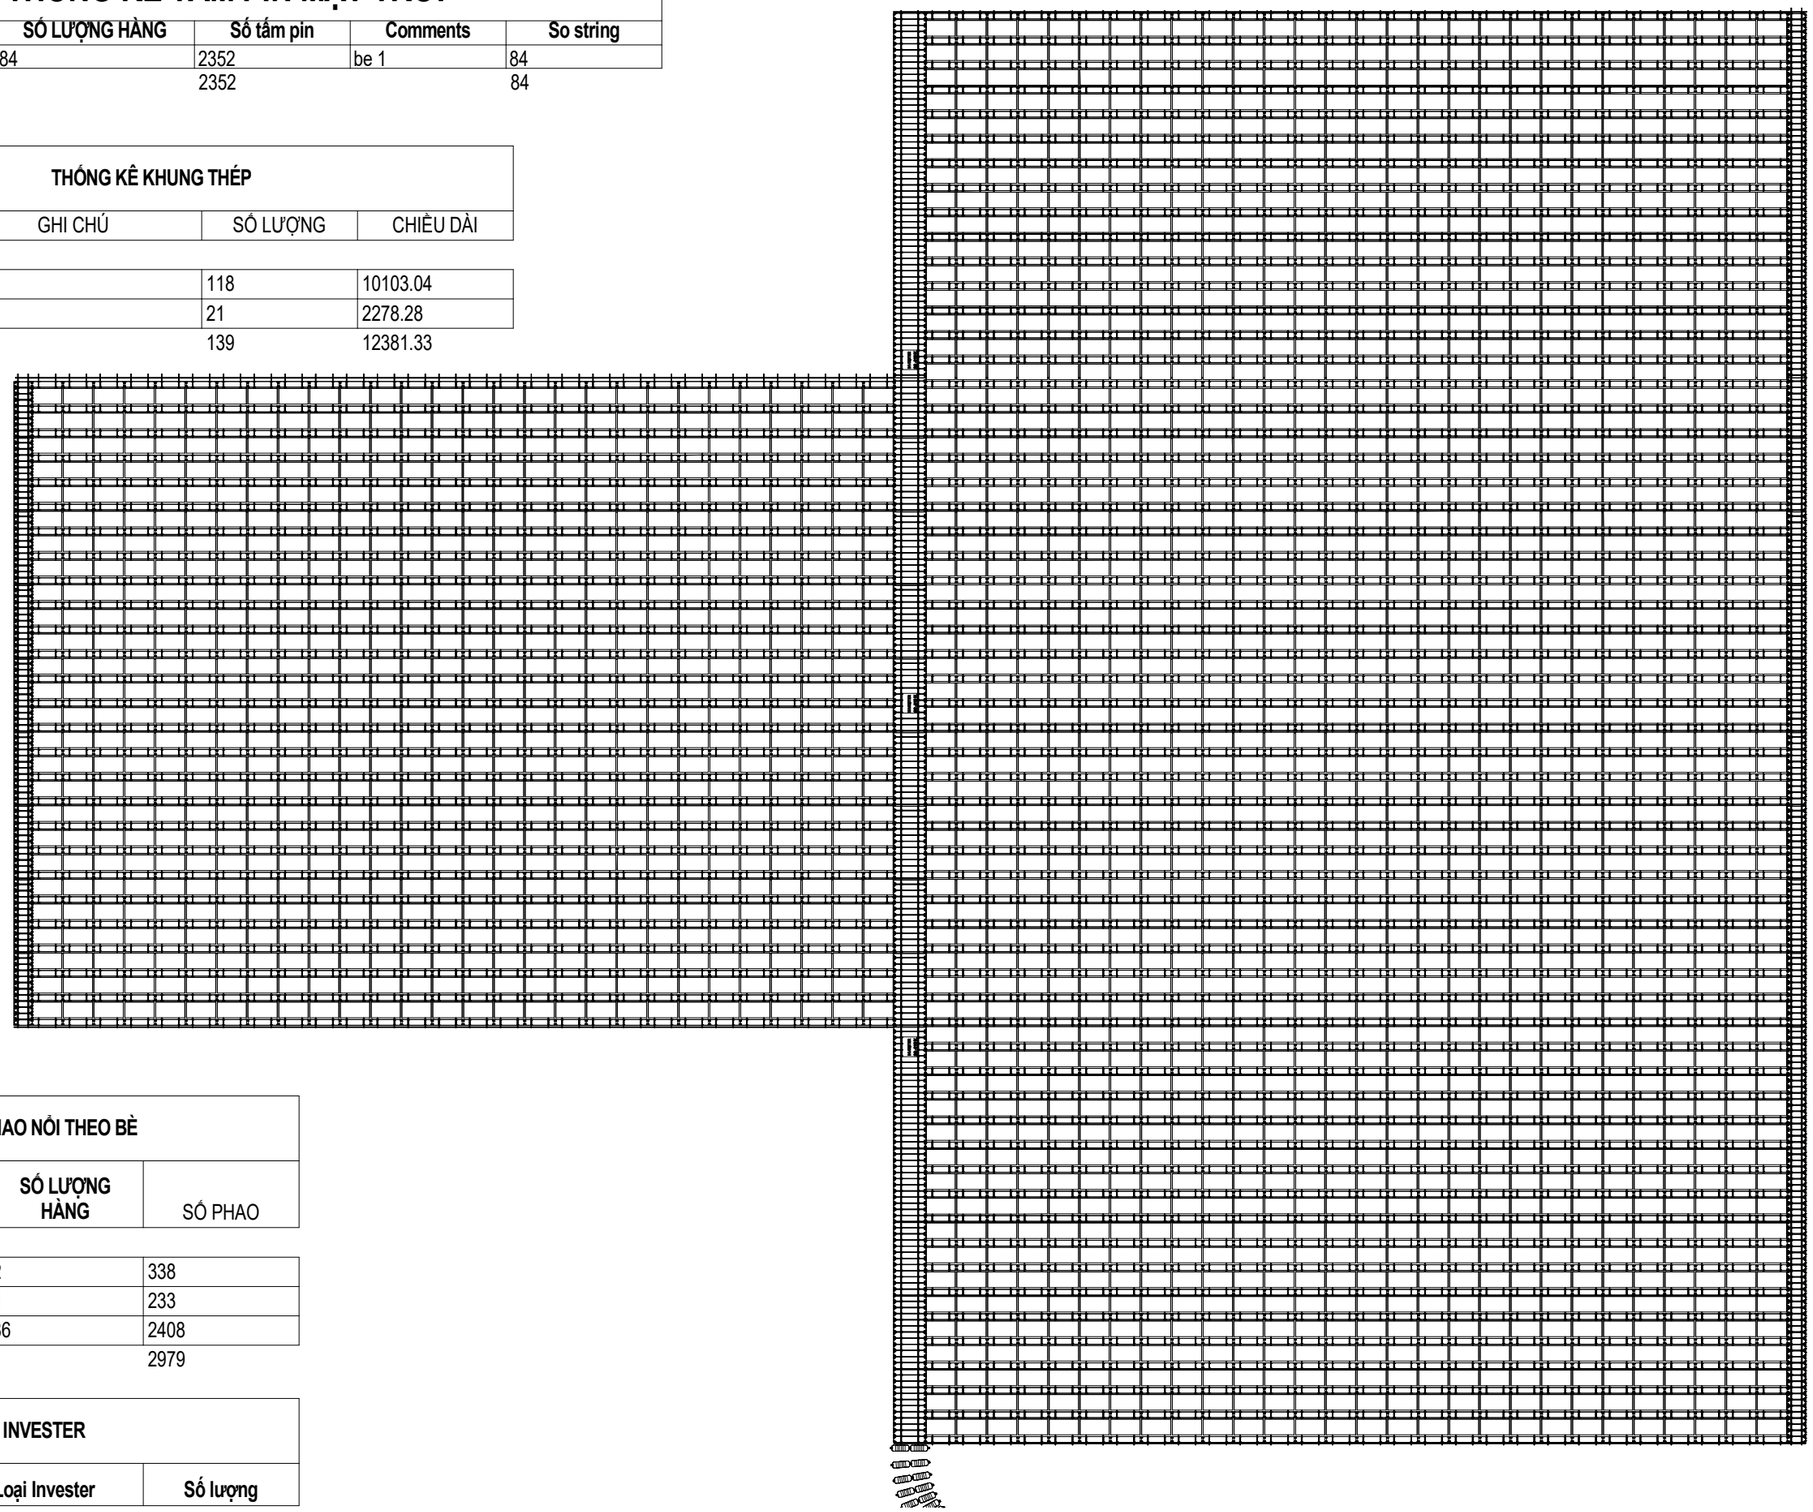

1 BỐ TRÍ BÈ PIN 01

1 : 500

SỬA REV.	NGÀY DATE	PHÊ DUYỆT APPRVD. BY	MÔ TẢ DESCRIPTION

N

DỰ ÁN / PROJECT:

CHỦ ĐẦU TƯ / INVESTOR:

TƯ VẤN QLDA & TVGS:

PHÊ DUYỆT/ APPROVED BY: | KÝ/ SIGN:

GIÁM SÁT THI CÔNG

NGƯỜI THỰC HIỆN: LÊ MINH NHẬT | KÝ/ SIGN:

HỒ SƠ / FILE:

HẠNG MỤC / ITEM: <None>

TÊN BẢN VẼ / DRAWING TITLE: Bố trí bè pin 1 Hồ Bản Mòng

TỶ LỆ / SCALE:	NGÀY / DATE:	HIỆU CHỈNH / REV.:
	.../2026	00

SỐ BẢN VẼ / DRAWING NO.: CT-BP-01

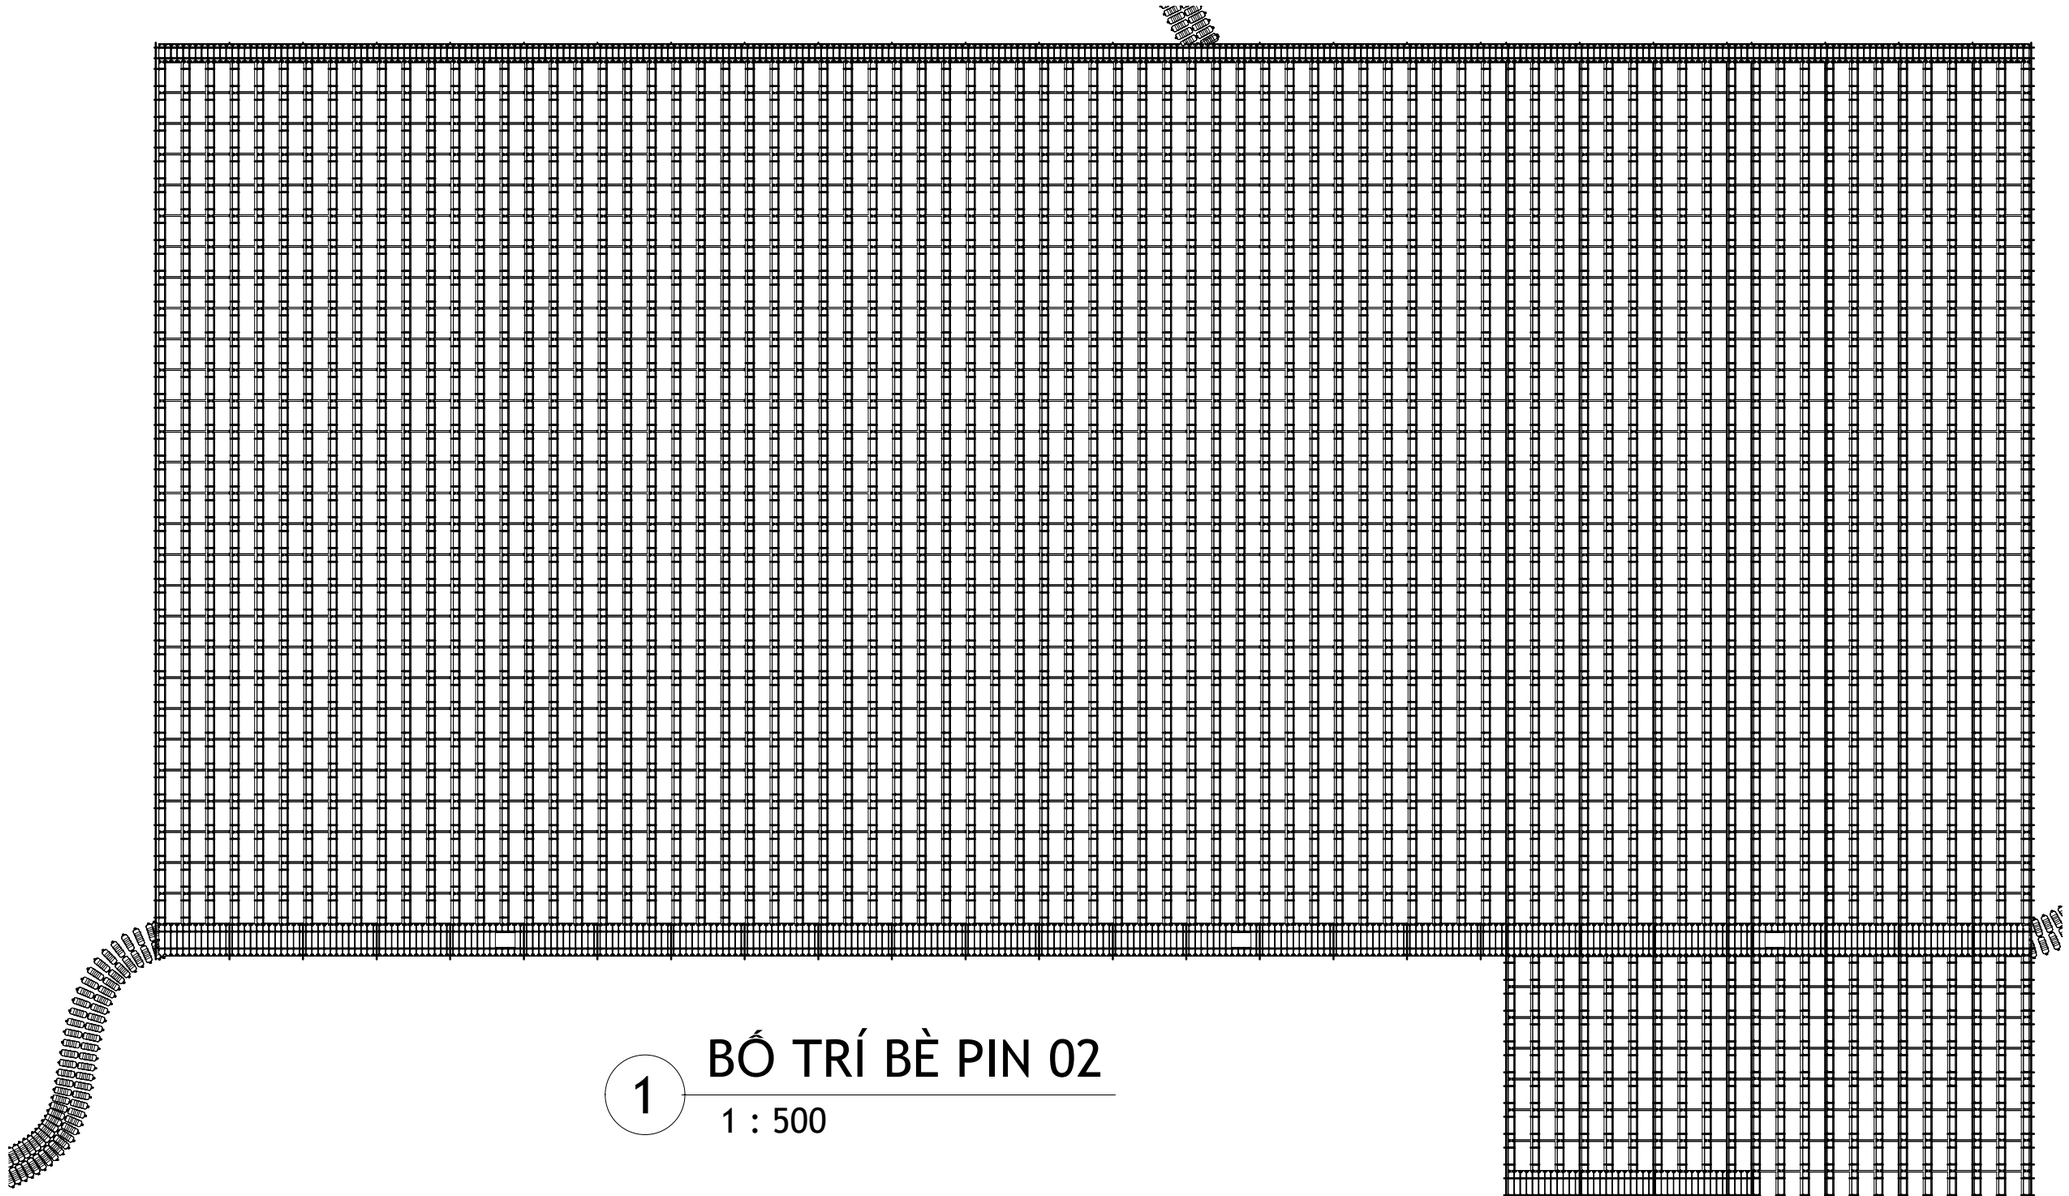

1 BỐ TRÍ BÈ PIN 02

1 : 500

THỐNG KÊ TẤM PIN MẶT TRỜI

Cấu kiện	SỐ LƯỢNG HÀNG	Số tấm pin	Comments	So string
DÃI PIN MẶT TRỜI	1	28	be 1	1
DÃI PIN MẶT TRỜI	97	2352	be 2	84
Grand total: 98		2380		85

THỐNG KÊ KHUNG THÉP

LOẠI	GHI CHÚ	SỐ LƯỢNG	CHIỀU DÀI
Dầm C52		90	10210.61
Hộp 40x60		36	3979.71
Grand total: 126		126	14190.32

SỐ PHAO NỔI THEO BÈ

DÃI PIN	SỐ LƯỢNG HÀNG	SỐ PHAO
DÃI PHAO ĐI LẠI	2	350
DÃI PHAO ĐI LẠI	2	345
DÃI PHAO ĐỠ PIN	100	2422
Grand total: 104		3117

INVESTER

Thiết bị	Loại Invester	Số lượng
Invester	SG -510HX	3
Grand total: 3		

SỬA REV.	NGÀY DATE	PHÊ DUYỆT APPRVD. BY	MÔ TẢ DESCRIPTION

N

DỰ ÁN / PROJECT:

CHỦ ĐẦU TƯ / INVESTOR:

TƯ VẤN QLDA & TVGS:

PHÊ DUYỆT/ APPROVED BY: | KÝ/ SIGN:

GIÁM SÁT THI CÔNG

NGƯỜI THỰC HIỆN: | KÝ/ SIGN:

LÊ MINH NHẬT

HỒ SƠ / FILE:

HẠNG MỤC / ITEM:

<None>

TÊN BẢN VẼ / DRAWING TITLE:

Bố trí bè pin 2 Hồ Bản Mòng

TỶ LỆ / SCALE:	NGÀY / DATE:	HIỆU CHỈNH / REV.:
	.../2026	00

SỐ BẢN VẼ / DRAWING NO.:

CT-BP-02

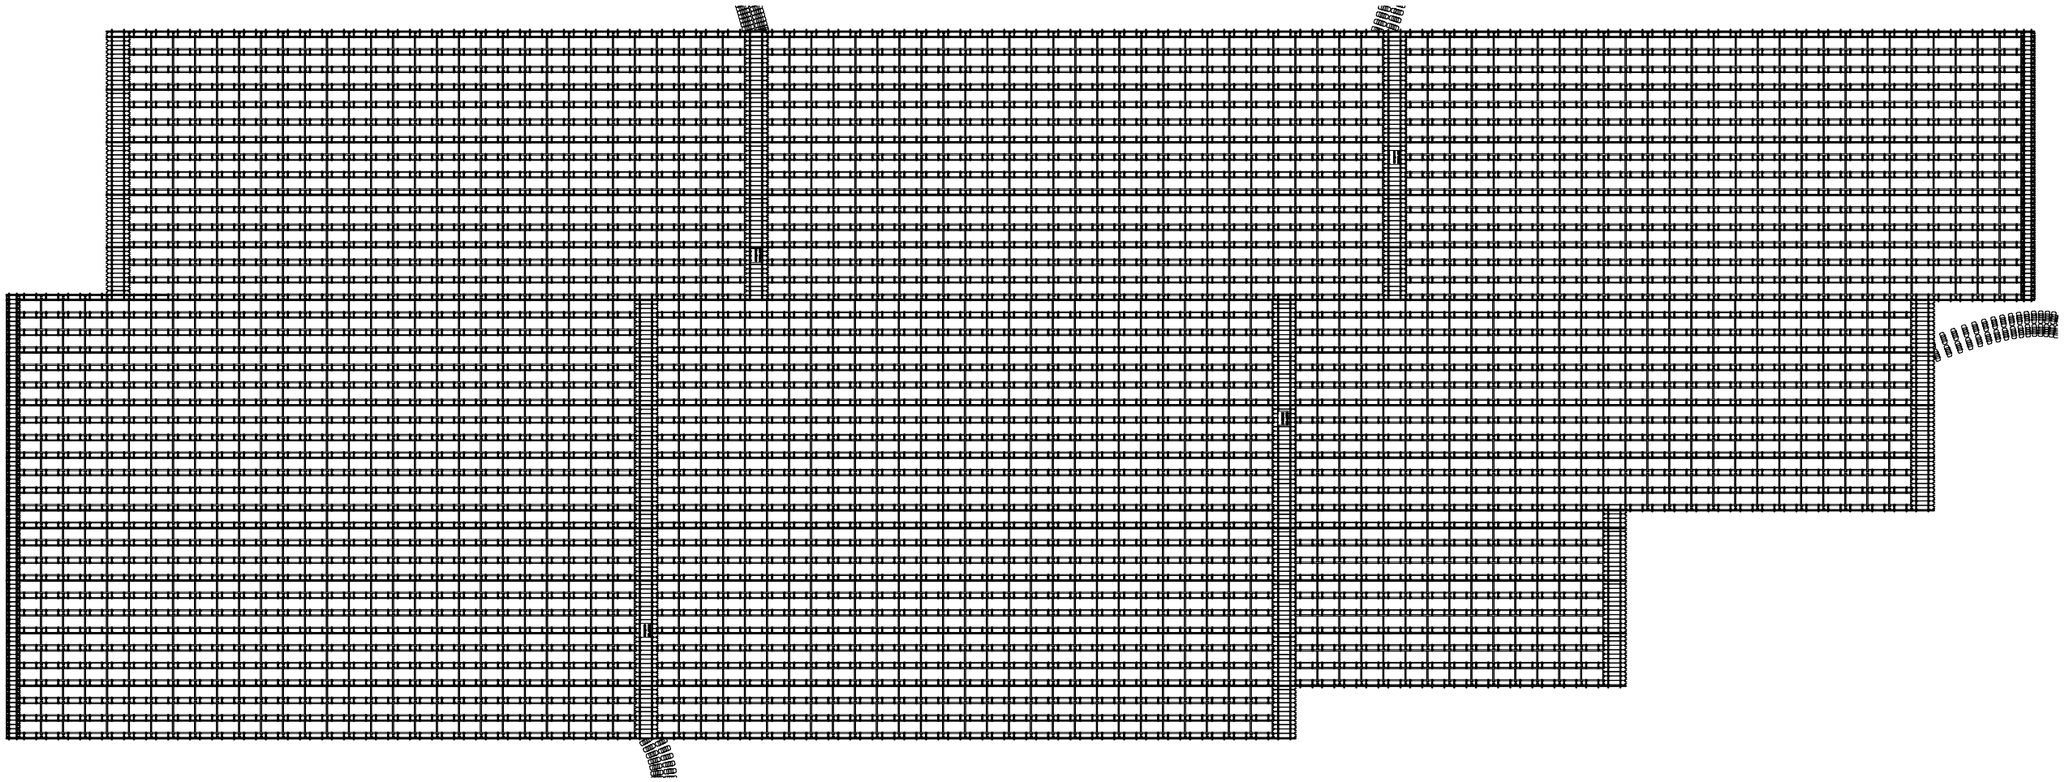

1 BỐ TRÍ BÈ PIN 03

1 : 700

THỐNG KÊ TẤM PIN MẶT TRỜI

Cấu kiện	SỐ LƯỢNG HÀNG	Số tấm pin	Comments	So string
DÃI PIN MẶT TRỜI	117	3136	be 3	112
Grand total: 117		3136		112

SỐ PHAO NỐI THEO BÈ		
DÃI PIN	SỐ LƯỢNG HÀNG	SỐ PHAO
DÃI PHAO ĐI LẠI	7	472
DÃI PHAO ĐI LẠI	2	162
DÃI PHAO ĐỠ PIN	121	3224
Grand total: 130		3858

THỐNG KÊ KHUNG THÉP			
LOẠI	GHI CHÚ	SỐ LƯỢNG	CHIỀU DÀI
Dầm C52		186	13355.70
Hộp 40x60		19	3558.71
Grand total: 205		205	16914.41

INVESTER		
Thiết bị	Loại Invester	Số lượng
Invester	SG -510HX	4
Grand total: 4		

SỬA REV.	NGÀY DATE	PHÊ DUYỆT APPRVD. BY	MÔ TẢ DESCRIPTION

N

DỰ ÁN / PROJECT:

CHỦ ĐẦU TƯ / INVESTOR:

TƯ VẤN QLDA & TVGS:

PHÊ DUYỆT/ APPROVED BY: | KÝ/ SIGN:

GIÁM SÁT THI CÔNG

NGƯỜI THỰC HIỆN: | KÝ/ SIGN:

LÊ MINH NHẬT

HỒ SƠ / FILE:

HẠNG MỤC / ITEM:

<None>

TÊN BẢN VẼ / DRAWING TITLE:

Bố trí bè pin 3 Hồ Bản Mòng

TỶ LỆ / SCALE:	NGÀY / DATE:	HIỆU CHỈNH / REV.:
	.../2026	00

SỐ BẢN VẼ / DRAWING NO.:

CT-BP-03

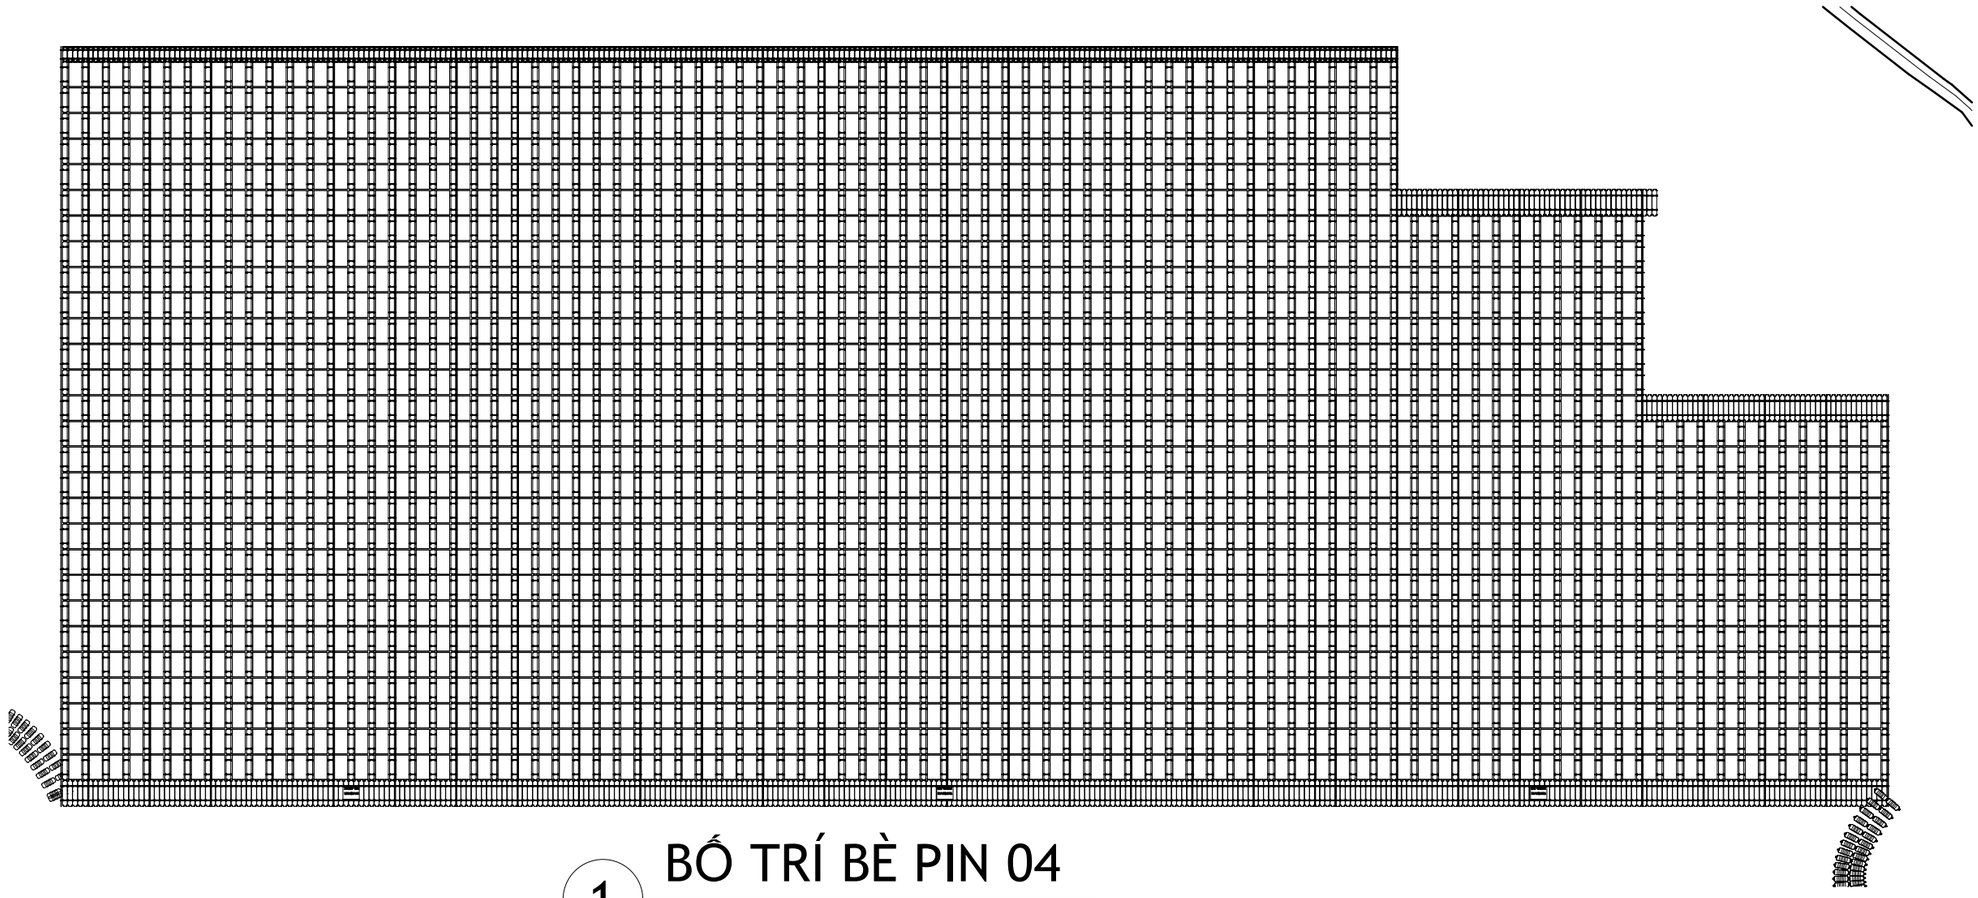

1 BỐ TRÍ BÈ PIN 04

1 : 600

THỐNG KÊ TẤM PIN MẶT TRỜI

Cấu kiện	SỐ LƯỢNG HÀNG	Số tấm pin	Comments	So string
DÃI PIN MẶT TRỜI	89	2252	be 4	80.428571
Grand total: 89		2252		80.428571

SỐ PHAO NỔI THEO BÈ		
DÃI PIN	SỐ LƯỢNG HÀNG	SỐ PHAO
DÃI PHAO ĐI LẠI	1	261
DÃI PHAO ĐI LẠI	5	729
DÃI PHAO ĐI LẠI	1	261
DÃI PHAO ĐỠ PIN	90	2280
Grand total: 97		3531

INVESTER		
Thiết bị	Loại Invester	Số lượng
Invester	SG -510HX	3
Grand total: 3		

THỐNG KÊ KHUNG THÉP			
LOẠI	GHI CHÚ	SỐ LƯỢNG	CHIỀU DÀI
Dầm C52		77	11690.48
Hộp 40x60		36	2962.08
Grand total: 113		113	14652.56

SỬA REV.	NGÀY DATE	PHÊ DUYỆT APPRVD. BY	MÔ TẢ DESCRIPTION

N

DỰ ÁN / PROJECT:

CHỦ ĐẦU TƯ / INVESTOR:

TƯ VẤN QLDA & TVGS:

PHÊ DUYỆT/ APPROVED BY: | KÝ/ SIGN:

GIÁM SÁT THI CÔNG

NGƯỜI THỰC HIỆN: LÊ MINH NHẬT | KÝ/ SIGN:

HỒ SƠ / FILE:

HẠNG MỤC / ITEM: <None>

TÊN BẢN VẼ / DRAWING TITLE: Bố trí bè pin 4 Hồ Bản Mòng

TỶ LỆ / SCALE:	NGÀY / DATE:	HIỆU CHỈNH / REV.:
	.../2026	00

SỐ BẢN VẼ / DRAWING NO.: CT-BP-04

SỬA REV.	NGÀY DATE	PHÊ DUYỆT APPRVD. BY	MÔ TẢ DESCRIPTION

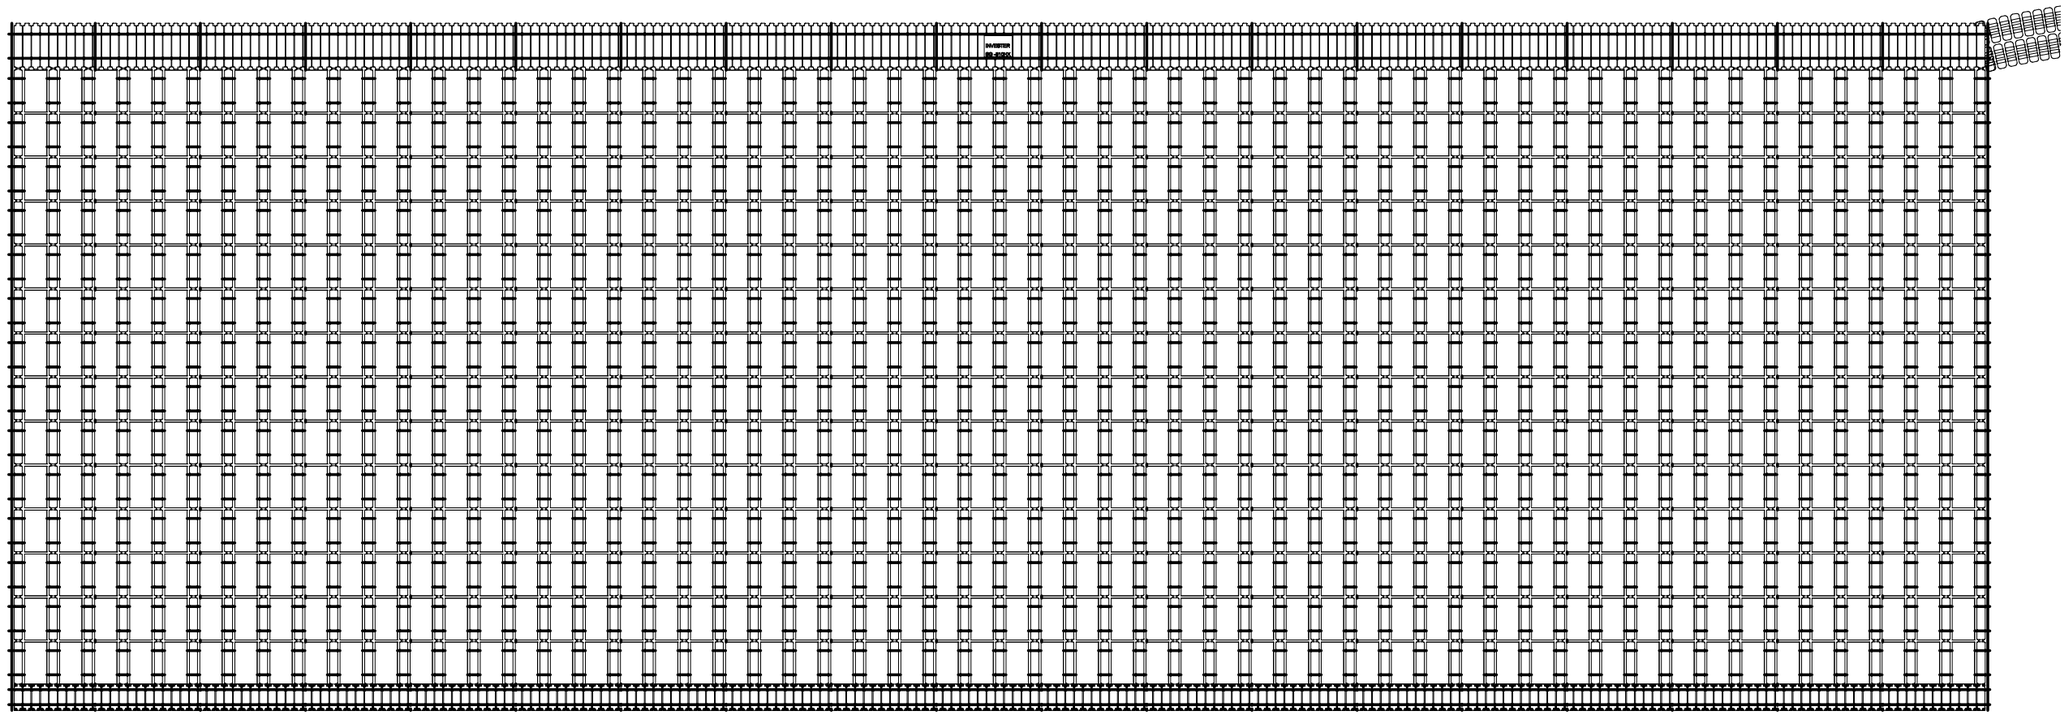

N

1 BỐ TRÍ BÈ PIN 05

1 : 350

THỐNG KÊ TẤM PIN MẶT TRỜI

Cấu kiện	SỐ LƯỢNG HÀNG	Số tấm pin	Comments	So string
DẢI PIN MẶT TRỜI	56	784	be 5	28
Grand total: 56		784		28

SỐ PHAO NỔI THEO BÈ		
DẢI PIN	SỐ LƯỢNG HÀNG	SỐ PHAO
DẢI PHAO ĐI LẠI	1	225
DẢI PHAO ĐI LẠI	1	225
DẢI PHAO ĐỠ PIN	57	798
Grand total: 59		1248

INVESTER		
Thiết bị	Loại Invester	Số lượng
Invester	SG -510HX	1
Grand total: 1		

THỐNG KÊ KHUNG THÉP			
LOẠI	GHI CHÚ	SỐ LƯỢNG	CHIỀU DÀI
Dầm C52		32	3617.52
Hộp 40x60		20	784.10
Grand total: 52		52	4401.62

DỰ ÁN / PROJECT:

CHỦ ĐẦU TƯ / INVESTOR:

TƯ VẤN QLDA & TVGS:

PHÊ DUYỆT/ APPROVED BY: | KÝ/ SIGN:

GIÁM SÁT THI CÔNG

NGƯỜI THỰC HIỆN: LÊ MINH NHẬT | KÝ/ SIGN:

HỒ SƠ / FILE:

HẠNG MỤC / ITEM: <None>

TÊN BẢN VẼ / DRAWING TITLE: Bố trí bè pin 5 Hồ Bản Mòng

TỶ LỆ / SCALE:	NGÀY / DATE:	HIỆU CHỈNH / REV.:
	.../2026	00

SỐ BẢN VẼ / DRAWING NO.: CT-BP-05

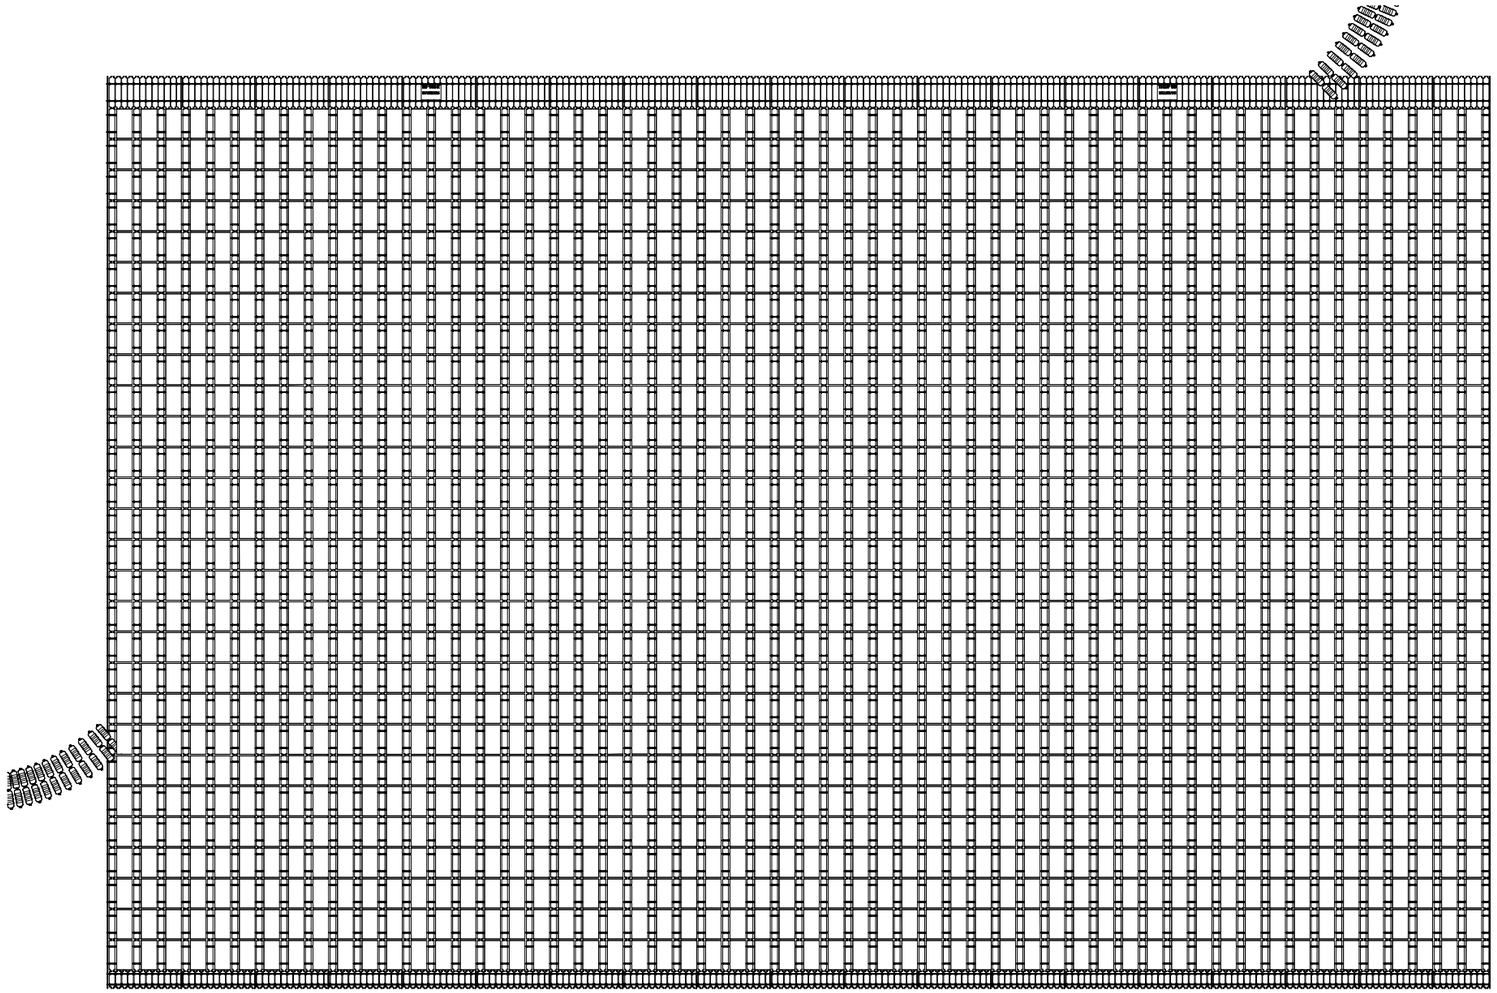

1 BỐ TRÍ BÈ PIN 06

1 : 500

THỐNG KÊ TẤM PIN MẶT TRỜI

Cấu kiện	SỐ LƯỢNG HÀNG	Số tấm pin	Comments	So string
DÃI PIN MẶT TRỜI	56	1568	be 6	56
Grand total: 56		1568		56

SỐ PHAO NỔI THEO BÈ

DÃI PIN	SỐ LƯỢNG HÀNG	SỐ PHAO
DÃI PHAO ĐI LẠI	1	225
DÃI PHAO ĐI LẠI	2	582
DÃI PHAO ĐỠ PIN	57	1596
Grand total: 60		2403

INVESTER

Thiết bị	Loại Invester	Số lượng
Invester	SG -510HX	2
Grand total: 2		

THỐNG KÊ KHUNG THÉP

LOẠI	GHI CHÚ	SỐ LƯỢNG	CHIỀU DÀI
Dầm C52		65	7660.56
Hộp 40x60		20	1486.40
Grand total: 85		85	9146.96

SỬA REV.	NGÀY DATE	PHÊ DUYỆT APPRVD. BY	MÔ TẢ DESCRIPTION

N

DỰ ÁN / PROJECT:

CHỦ ĐẦU TƯ / INVESTOR:

TƯ VẤN QLDA & TVGS:

PHÊ DUYỆT/ APPROVED BY: | KÝ/ SIGN:

GIÁM SÁT THI CÔNG

NGƯỜI THỰC HIỆN: LÊ MINH NHẬT | KÝ/ SIGN:

HỒ SƠ / FILE:

HẠNG MỤC / ITEM: <None>

TÊN BẢN VẼ / DRAWING TITLE: Bố trí bè pin 6 Hồ Bản Mòng

TỶ LỆ / SCALE:	NGÀY / DATE:	HIỆU CHỈNH / REV.:
	.../2026	00

SỐ BẢN VẼ / DRAWING NO.: CT-BP-06

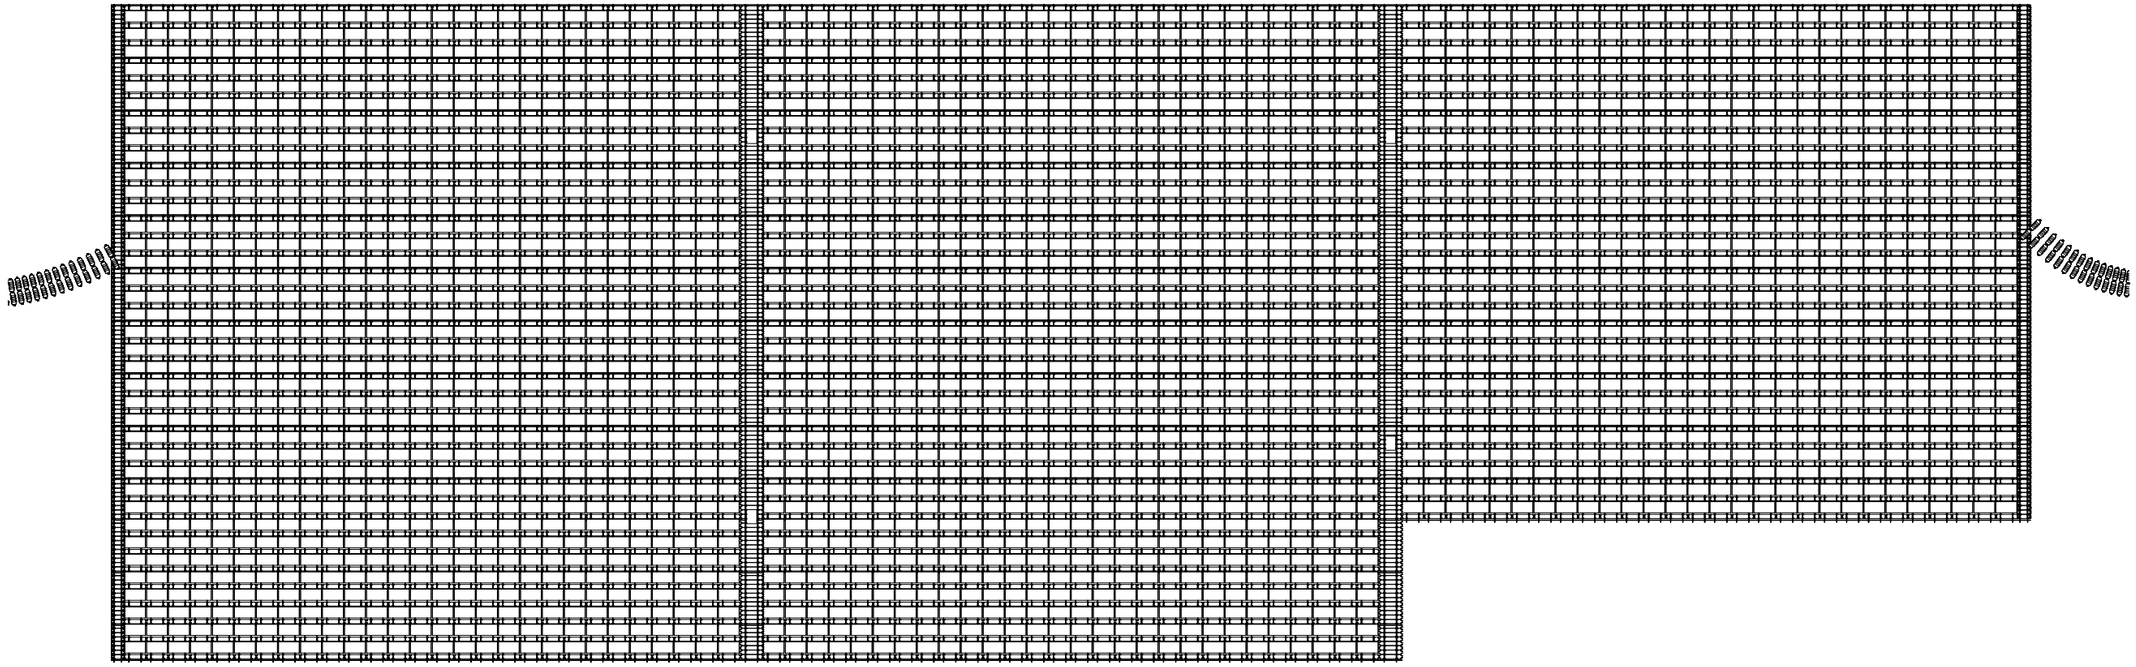

1 BỐ TRÍ BÈ PIN 07

1 : 700

THỐNG KÊ TẤM PIN MẶT TRỜI

Cấu kiện	SỐ LƯỢNG HÀNG	Số tấm pin	Comments	So string
DÃI PIN MẶT TRỜI	103	2884	be 7	103
Grand total: 103		2884		103

SỐ PHAO NỔI THEO BÈ		
DÃI PIN	SỐ LƯỢNG HÀNG	SỐ PHAO
DÃI PHAO ĐI LẠI	2	266
DÃI PHAO ĐI LẠI	2	298
DÃI PHAO ĐỠ PIN	106	2968
Grand total: 110		3532

INVESTER		
Thiết bị	Loại Invester	Số lượng
Invester	SG -510HX	4
Grand total: 4		

THỐNG KÊ KHUNG THÉP			
LOẠI	GHI CHÚ	SỐ LƯỢNG	CHIỀU DÀI
Dầm C52		176	12283.55
Hộp 40x60		14	2851.12
Grand total: 190		190	15134.67

SỬA REV.	NGÀY DATE	PHÊ DUYỆT APPRVD. BY	MÔ TẢ DESCRIPTION

N

DỰ ÁN / PROJECT:

CHỦ ĐẦU TƯ / INVESTOR:

TƯ VẤN QLDA & TVGS:

PHÊ DUYỆT/ APPROVED BY: | KÝ/ SIGN:

GIÁM SÁT THI CÔNG

NGƯỜI THỰC HIỆN: LÊ MINH NHẬT | KÝ/ SIGN:

HỒ SƠ / FILE:

HẠNG MỤC / ITEM: <None>

TÊN BẢN VẼ / DRAWING TITLE: Bố trí bè pin 7 Hồ Bản Mòng

TỶ LỆ / SCALE:	NGÀY / DATE:	HIỆU CHỈNH / REV.:
	.../2026	00

SỐ BẢN VẼ / DRAWING NO.: CT-BP-07

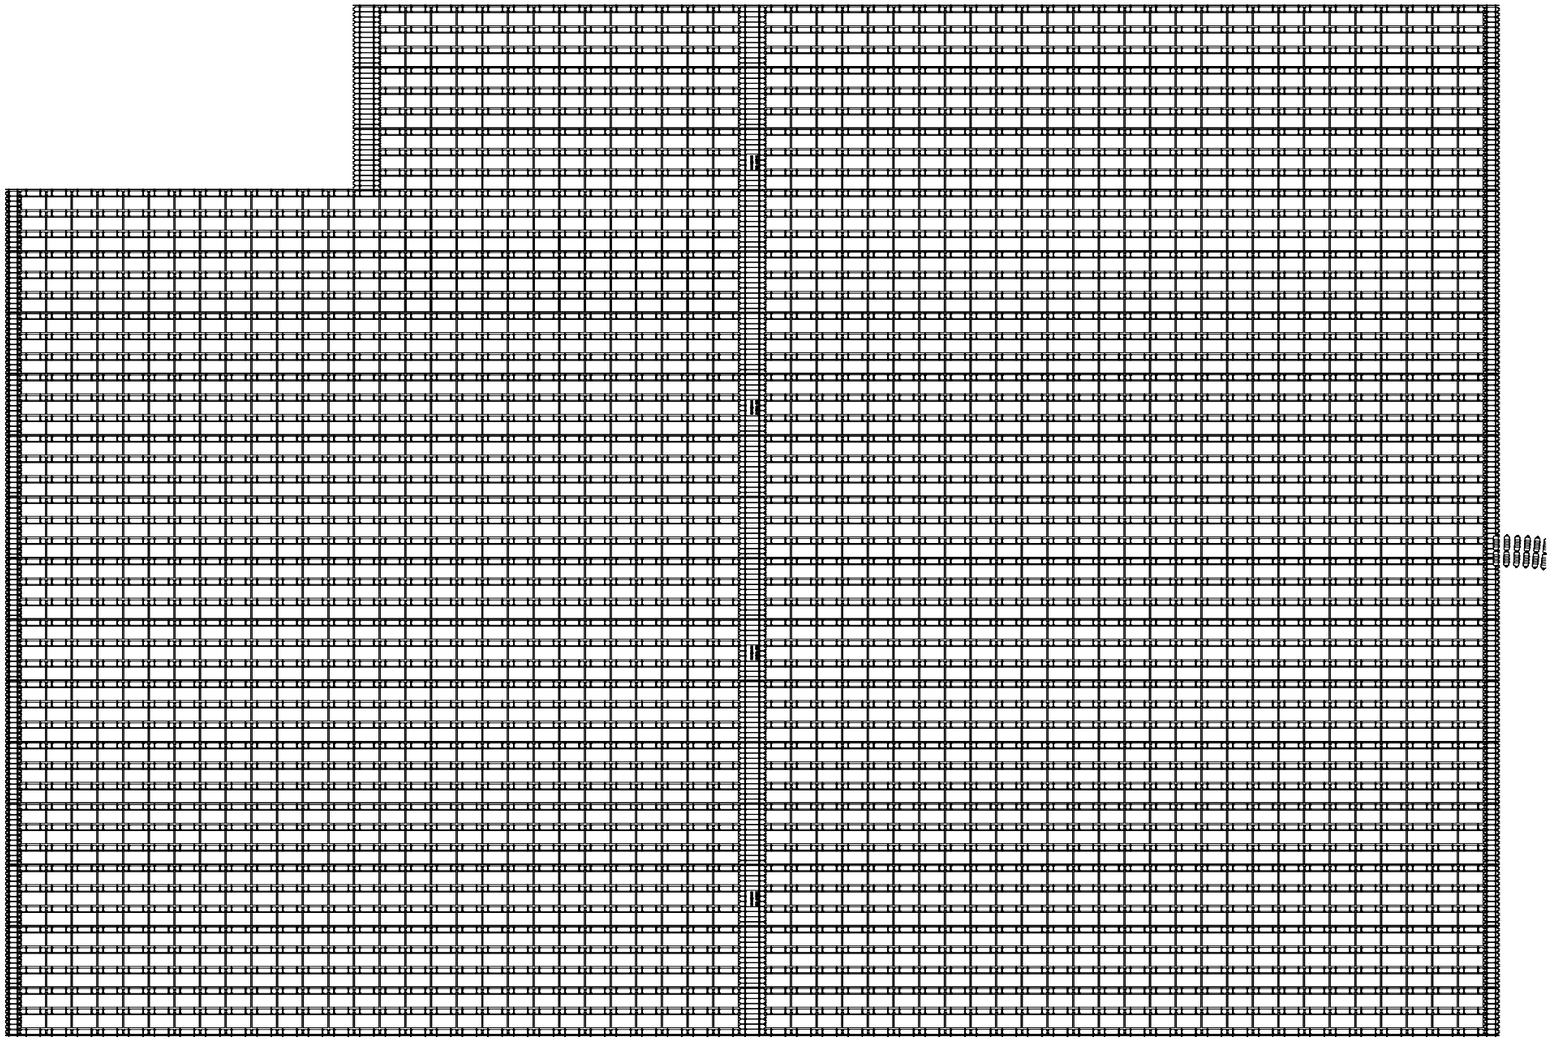

1 BỐ TRÍ BÈ PIN 08

1 : 600

THỐNG KÊ TẤM PIN MẶT TRỜI

Cấu kiện	SỐ LƯỢNG HÀNG	Số tấm pin	Comments	So string
DÃI PIN MẶT TRỜI	110	2884	be 8	103
Grand total: 110		2884		103

SỐ PHAO NỔI THEO BÈ

DÃI PIN	SỐ LƯỢNG HÀNG	SỐ PHAO
DÃI PHAO ĐI LẠI	2	366
DÃI PHAO ĐI LẠI	2	237
DÃI PHAO ĐỠ PIN	102	2730
Grand total: 106		3333

INVESTER

Thiết bị	Loại Invester	Số lượng
Invester	SG -510HX	4
Grand total: 4		

THỐNG KÊ KHUNG THÉP

LOẠI	GHI CHÚ	SỐ LƯỢNG	CHIỀU DÀI
Dầm C52		118	11401.31
Hộp 40x60		18	2527.33
Grand total: 136		136	13928.65

SỬA REV.	NGÀY DATE	PHÊ DUYỆT APPRVD. BY	MÔ TẢ DESCRIPTION

N

DỰ ÁN / PROJECT:

CHỦ ĐẦU TƯ / INVESTOR:

TƯ VẤN QLDA & TVGS:

PHÊ DUYỆT/ APPROVED BY: | KÝ/ SIGN:

GIÁM SÁT THI CÔNG

NGƯỜI THỰC HIỆN: LÊ MINH NHẬT | KÝ/ SIGN:

HỒ SƠ / FILE:

HẠNG MỤC / ITEM: <None>

TÊN BẢN VẼ / DRAWING TITLE: Bố trí bè pin 8 Hồ Bản Mòng

TỶ LỆ / SCALE:	NGÀY / DATE:	HIỆU CHỈNH / REV.:
	.../2026	00

SỐ BẢN VẼ / DRAWING NO.: CT-BP-08

SỐ PHAO ĐỠ CÁP		
DẢI PIN	**SỐ LƯỢNG HÀNG**	SỐ PHAO
ĐỠ CÁP	707	1414
Grand total: 707		1414

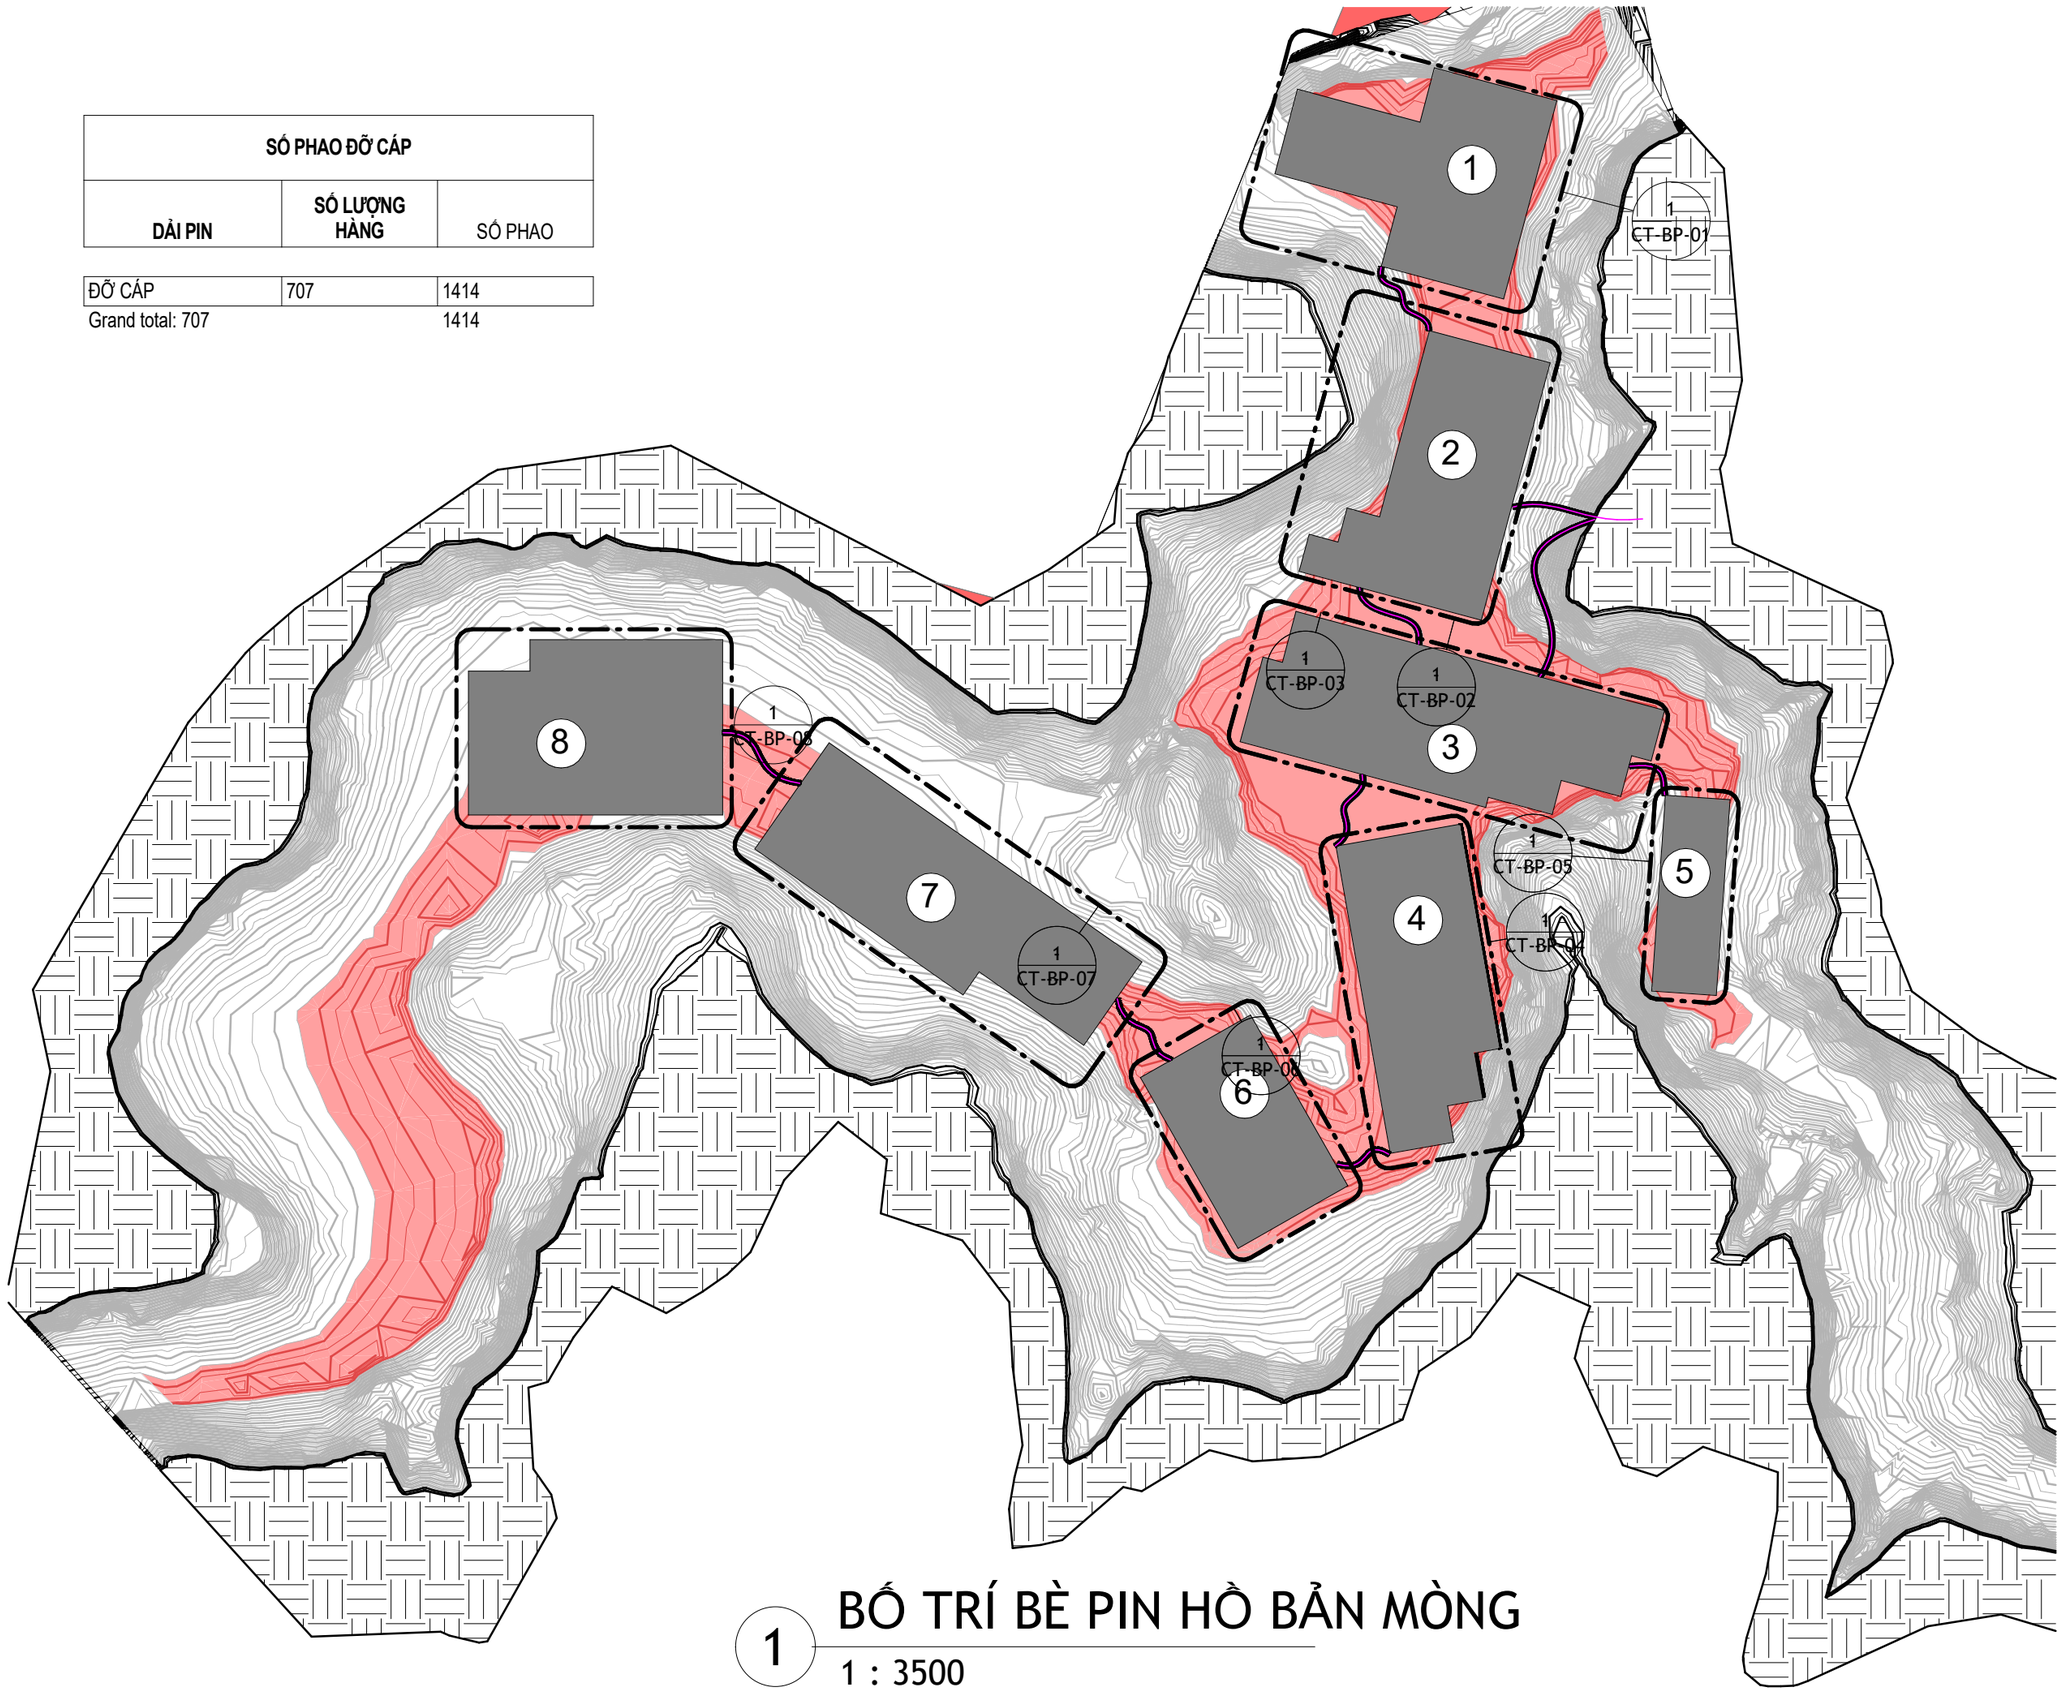

1 BỐ TRÍ BÈ PIN HỒ BẢN MÒNG

1 : 3500

SỬA REV.	NGÀY DATE	PHÊ DUYỆT APPRVD. BY	MÔ TẢ DESCRIPTION

N

DỰ ÁN / PROJECT:

CHỦ ĐẦU TƯ / INVESTOR:

TƯ VẤN QLDA & TVGS:

PHÊ DUYỆT/ APPROVED BY: | KÝ/ SIGN:

GIÁM SÁT THI CÔNG

NGƯỜI THỰC HIỆN: | KÝ/ SIGN:

LÊ MINH NHẬT

HỒ SƠ / FILE:

HẠNG MỤC / ITEM:

<None>

TÊN BẢN VẼ / DRAWING TITLE:

Bố trí bè pin Hồ Bản Mòng

TỶ LỆ / SCALE:	NGÀY / DATE:	HIỆU CHỈNH / REV.:
	.../2026	00

SỐ BẢN VẼ / DRAWING NO.:

MB-B01-01