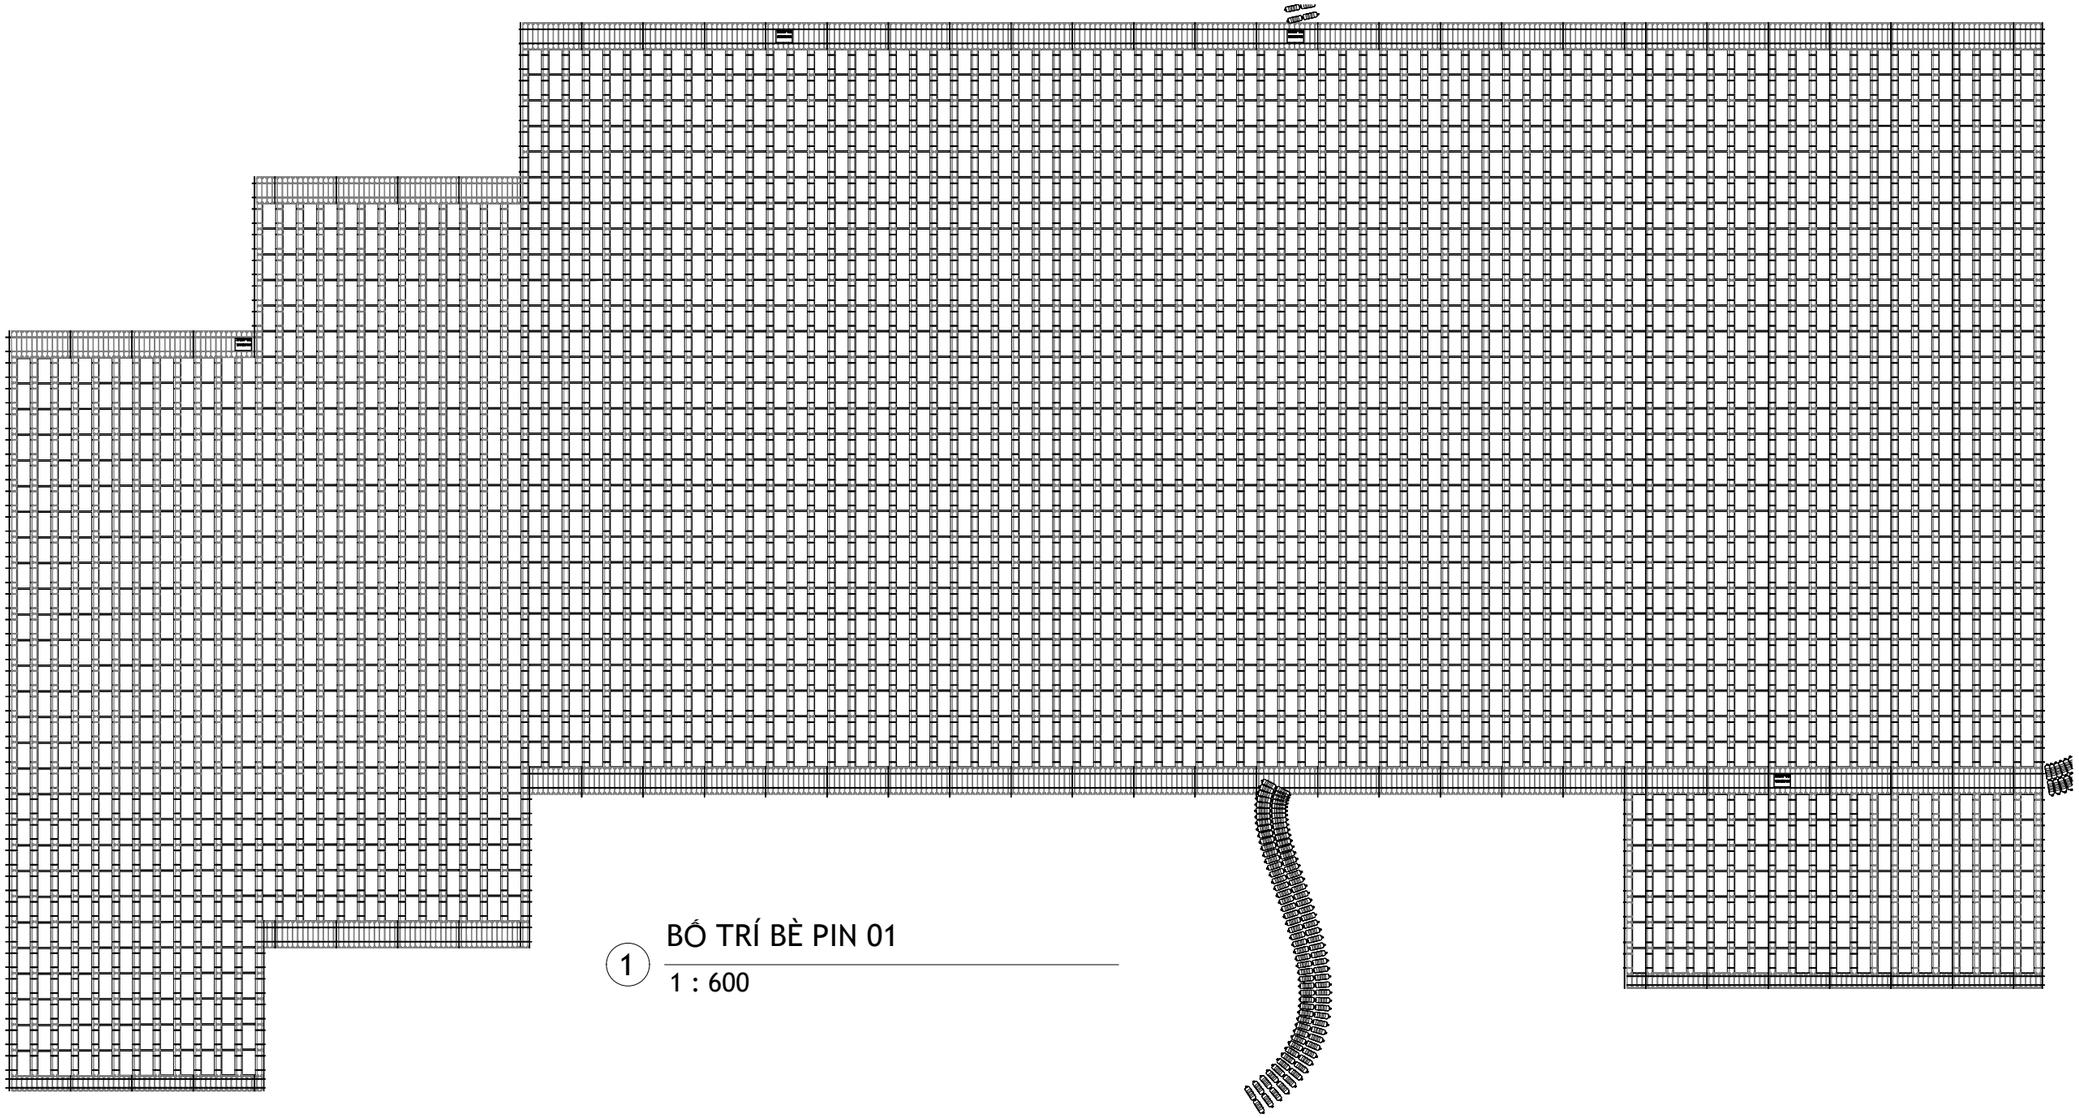

1 BỐ TRÍ BÈ PIN 01

1 : 600

SỐ PHAO NỔI THEO BÈ			
Family	**DẢI PIN**	**SỐ LƯỢNG HÀNG**	SỐ PHAO
Dai phaodi lai	DẢI PHAO ĐI LẠI	2	130
Dải phao đi lại kèm đỡ invester	DẢI PHAO ĐI LẠI	5	746
Dai phao do pin	DẢI PHAO ĐỠ PIN	122	2958
Grand total: 129			3834

INVESTER		
Thiết bị	**Loại Invester**	**Số lượng**
Invester	SG -510HX	4
Grand total: 4		

THỐNG KÊ TẤM PIN MẶT TRỜI				
Cấu kiện	**SỐ LƯỢNG HÀNG**	**Số tấm pin**	**Comments**	**So string**
DẢI PIN MẶT TRỜI	119	2912	be 2	104
Grand total: 119		2912		104

SỬA REV.	NGÀY DATE	PHÊ DUYỆT APPRVD. BY	MÔ TẢ DESCRIPTION

N

DỰ ÁN / PROJECT:

CHỦ ĐẦU TƯ / INVESTOR:

TƯ VẤN QLDA & TVGS:

PHÊ DUYỆT/ APPROVED BY: | KÝ/ SIGN:

GIÁM SÁT THI CÔNG

NGƯỜI THỰC HIỆN: LÊ MINH NHẬT | KÝ/ SIGN:

HỒ SƠ / FILE:

HẠNG MỤC / ITEM: <None>

TÊN BẢN VẼ / DRAWING TITLE: Bố trí bè pin 1 Hồ Bản Mòng

TỶ LỆ / SCALE:	NGÀY / DATE:	HIỆU CHỈNH / REV.:
	.../2026	00

SỐ BẢN VẼ / DRAWING NO.: CT-BP-01

SỐ PHAO ĐỠ CÁP		
DÃI PIN	**SỐ LƯỢNG HÀNG**	SỐ PHAO
ĐỠ CÁP	1327	2654
Grand total: 1327		2654

CÁP ĐIỆN ĐI TRÊN BỜ VÀ LUỒN QUA BÈ

CÁP ĐIỆN ĐI TRÊN BÈ PHAO

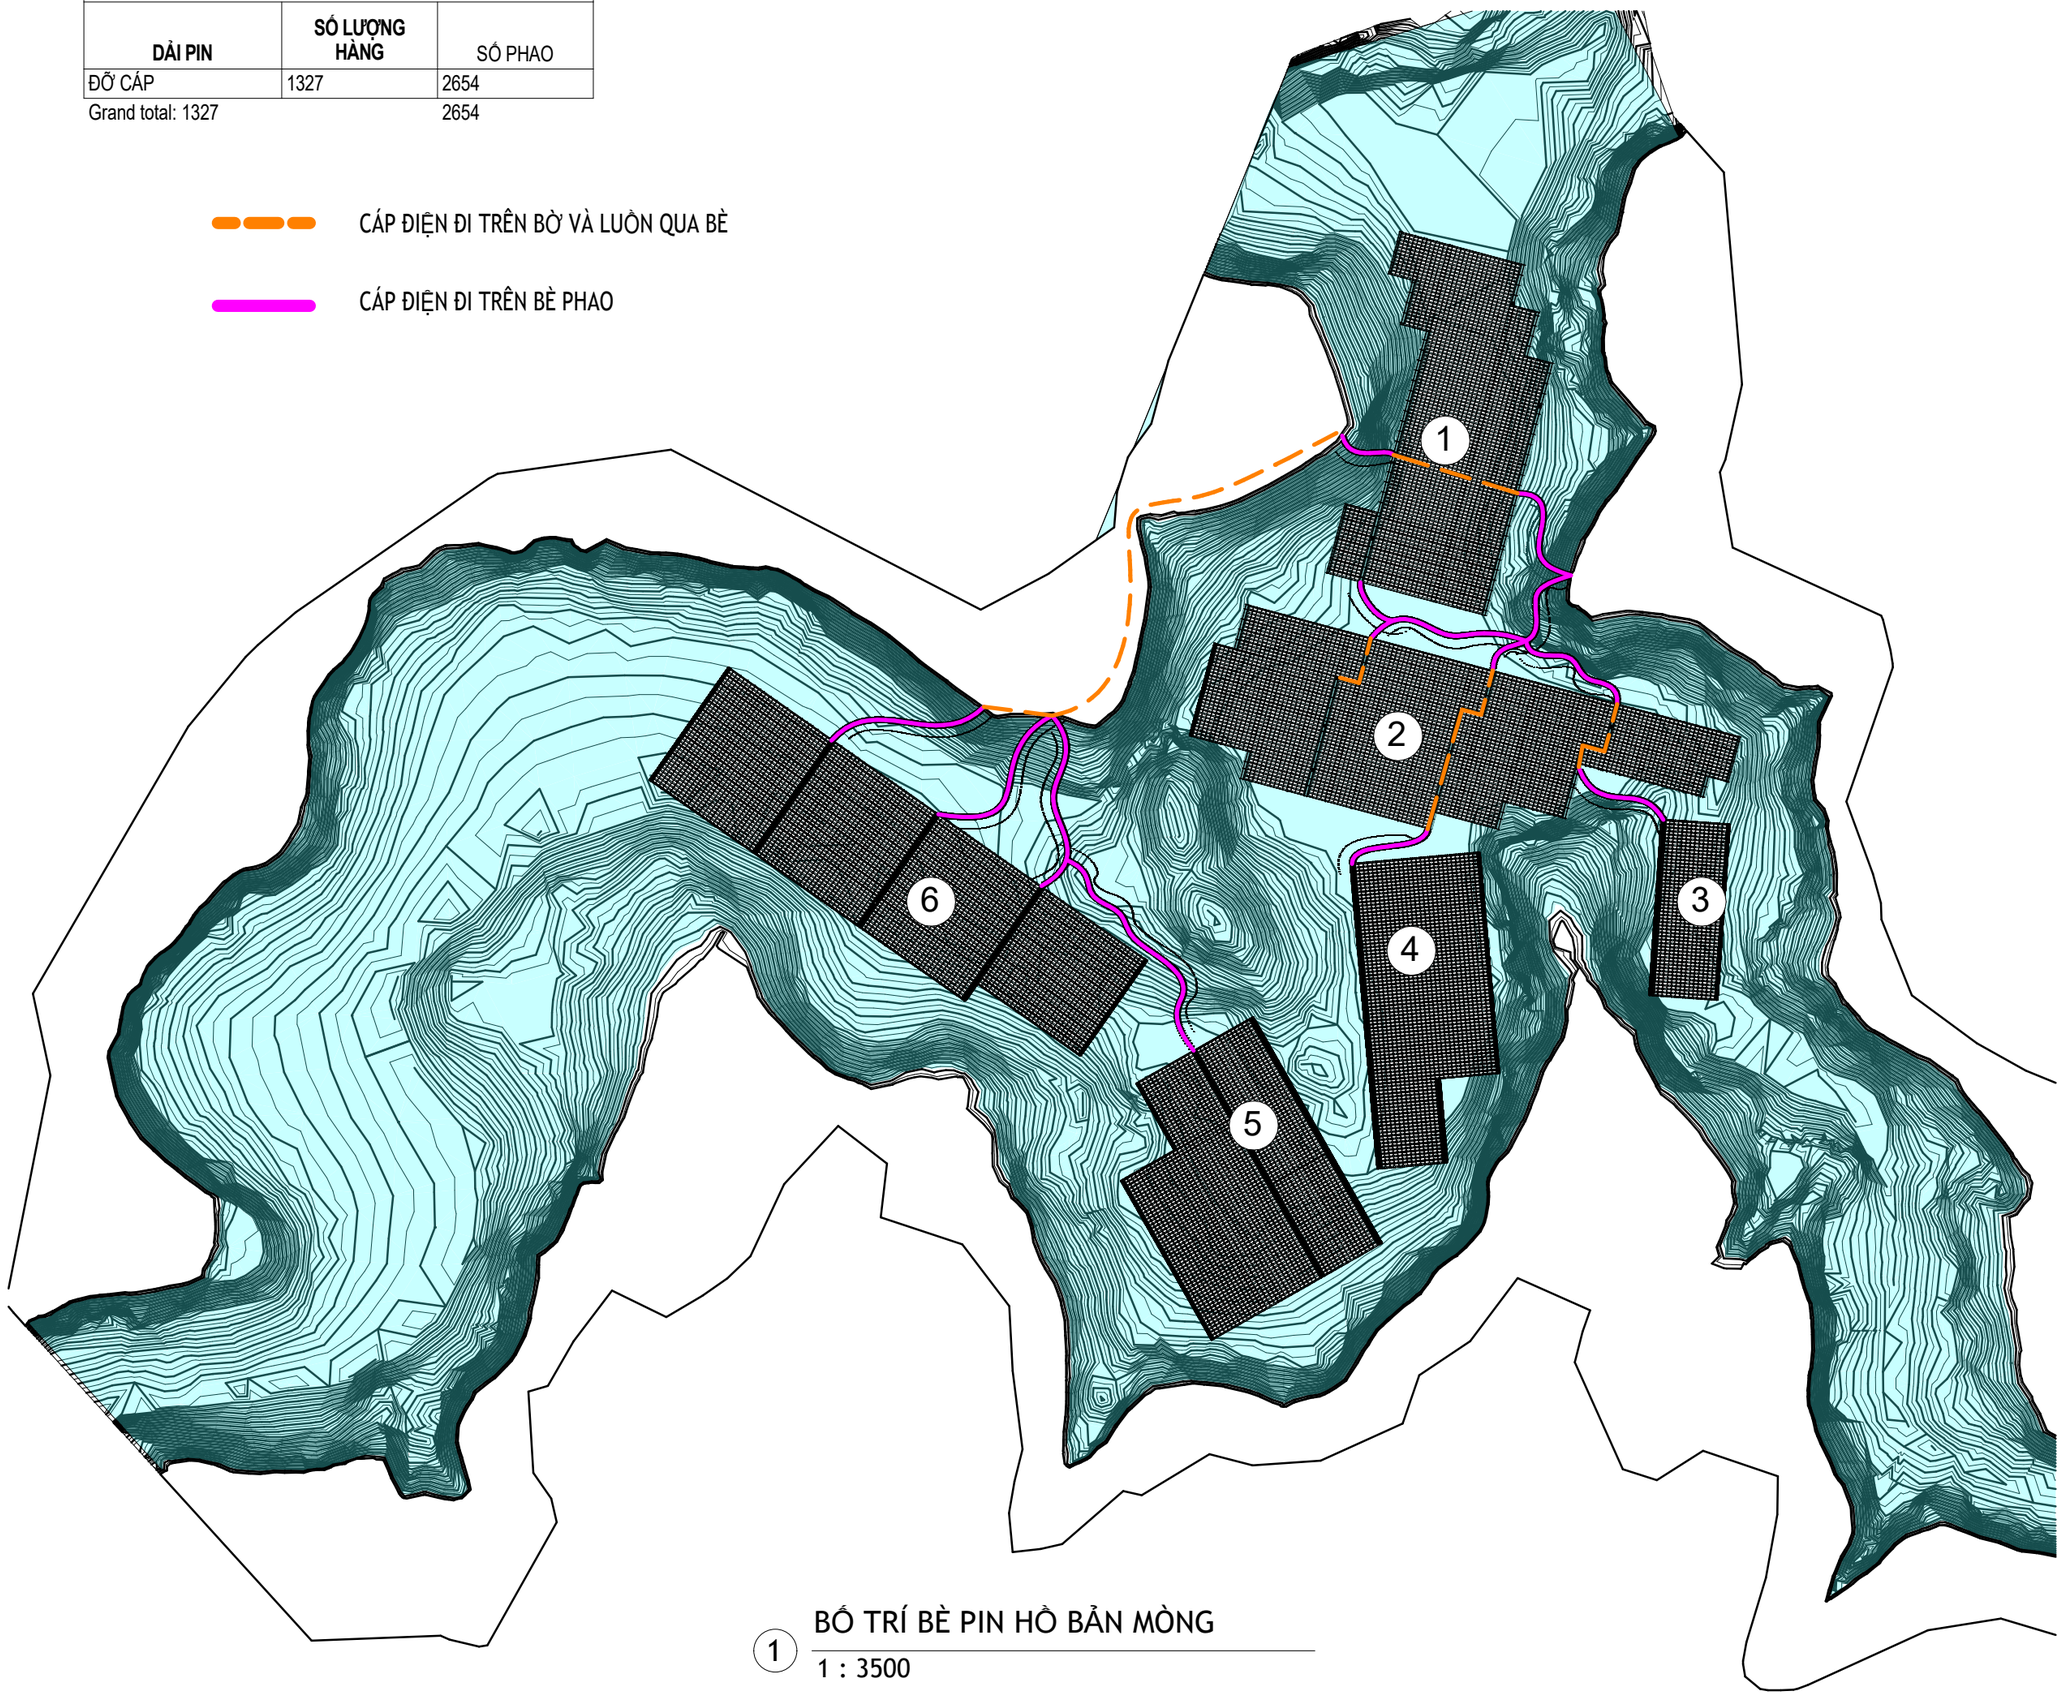

1 BỐ TRÍ BÈ PIN HỒ BẢN MÒNG

1 : 3500

SỬA REV.	NGÀY DATE	PHÊ DUYỆT APPRVD. BY	MÔ TẢ DESCRIPTION

N

DỰ ÁN / PROJECT:

CHỦ ĐẦU TƯ / INVESTOR:

TƯ VẤN QLDA & TVGS:

PHÊ DUYỆT/ APPROVED BY: | KÝ/ SIGN:

GIÁM SÁT THI CÔNG

NGƯỜI THỰC HIỆN: | KÝ/ SIGN:

LÊ MINH NHẬT

HỒ SƠ / FILE:

HẠNG MỤC / ITEM:

<None>

TÊN BẢN VẼ / DRAWING TITLE:

Bố trí bè pin Hồ Bản Mòng

TỶ LỆ / SCALE:	NGÀY / DATE:	HIỆU CHỈNH / REV.:
	.../2026	00

SỐ BẢN VẼ / DRAWING NO.:

MB-B01-01

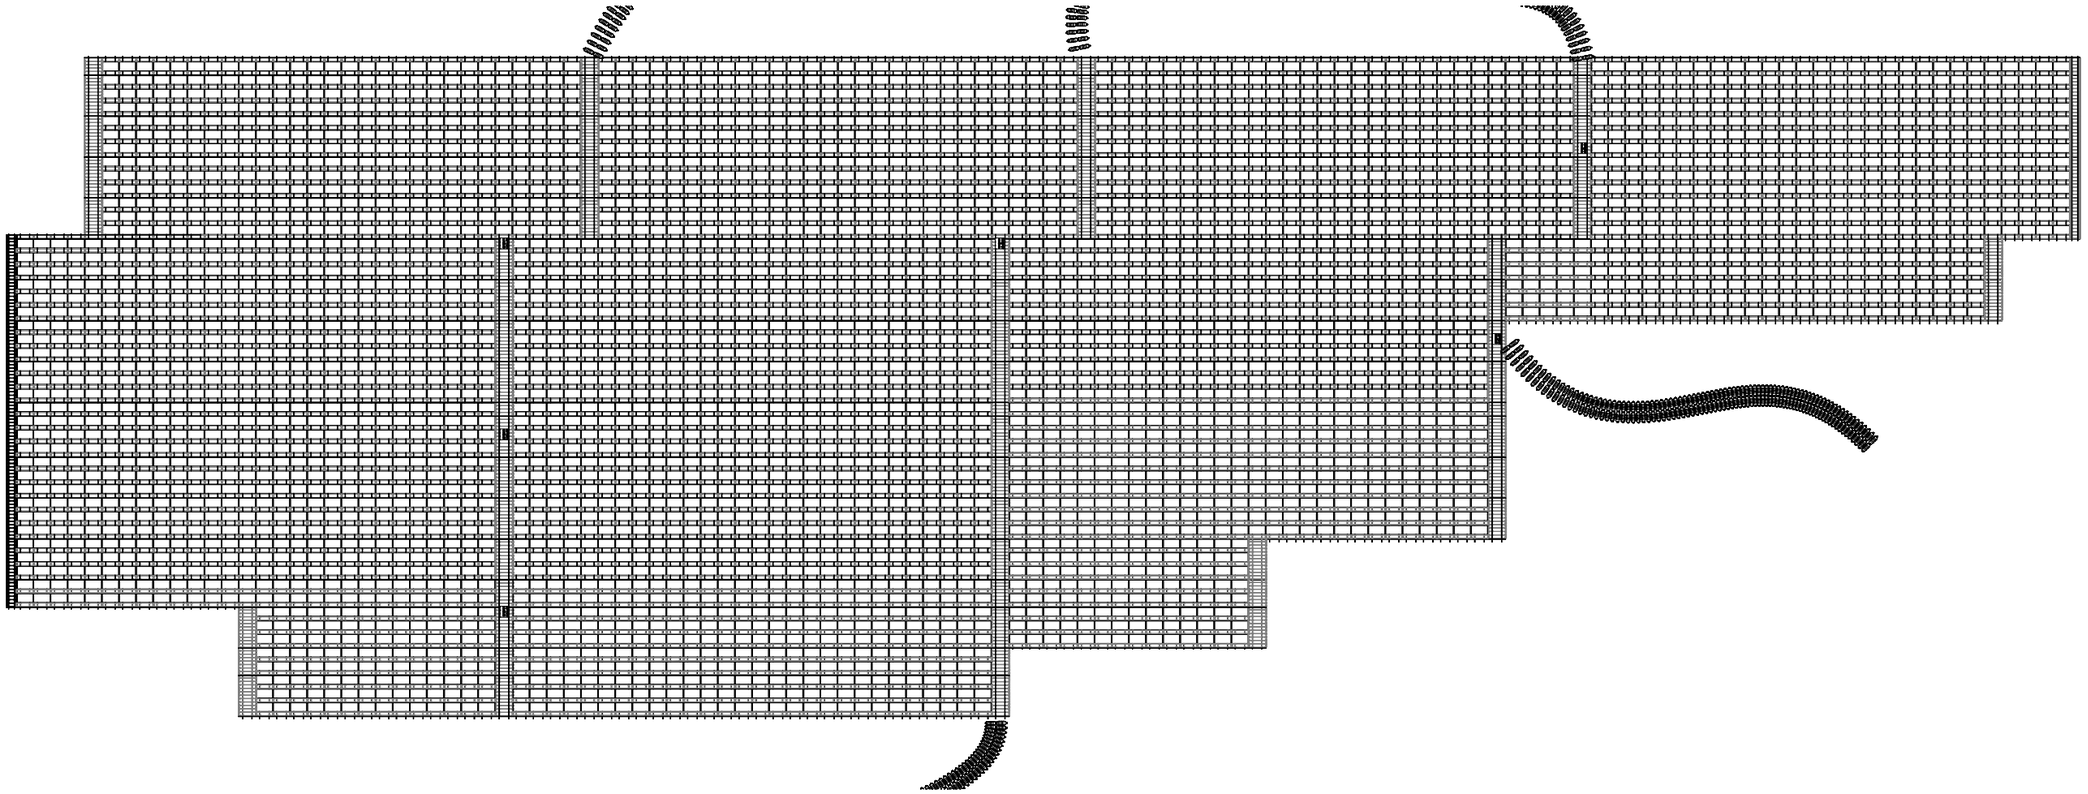

1 BỐ TRÍ BÈ PIN 02

1 : 900

SỐ PHAO NỔI THEO BÈ			
Family	**DẢI PIN**	**SỐ LƯỢNG HÀNG**	SỐ PHAO
Dai phaodi lai	DẢI PHAO ĐI LẠI	2	162
Dải phao đi lại kèm đỡ invester	DẢI PHAO ĐI LẠI	10	668
Dai phao do pin	DẢI PHAO ĐỠ PIN	162	4317
Grand total: 174			5147

INVESTER		
Thiết bị	**Loại Invester**	**Số lượng**
Invester	SG -510HX	6
Grand total: 6		

THỐNG KÊ TẤM PIN MẶT TRỜI				
Cấu kiện	**SỐ LƯỢNG HÀNG**	**Số tấm pin**	**Comments**	**So string**
DẢI PIN MẶT TRỜI	158	4200	be 3	150
Grand total: 158		4200		150

SỬA REV.	NGÀY DATE	PHÊ DUYỆT APPRVD. BY	MÔ TẢ DESCRIPTION

N

DỰ ÁN / PROJECT:

CHỦ ĐẦU TƯ / INVESTOR:

TƯ VẤN QLDA & TVGS:

PHÊ DUYỆT/ APPROVED BY: | KÝ/ SIGN:

GIÁM SÁT THI CÔNG

NGƯỜI THỰC HIỆN: | KÝ/ SIGN:

LÊ MINH NHẬT

HỒ SƠ / FILE:

HẠNG MỤC / ITEM:

<None>

TÊN BẢN VẼ / DRAWING TITLE:

Bố trí bè pin 2 Hồ Bản Mòng

TỶ LỆ / SCALE:	NGÀY / DATE:	HIỆU CHỈNH / REV.:
	.../2026	00

SỐ BẢN VẼ / DRAWING NO.:

CT-BP-02

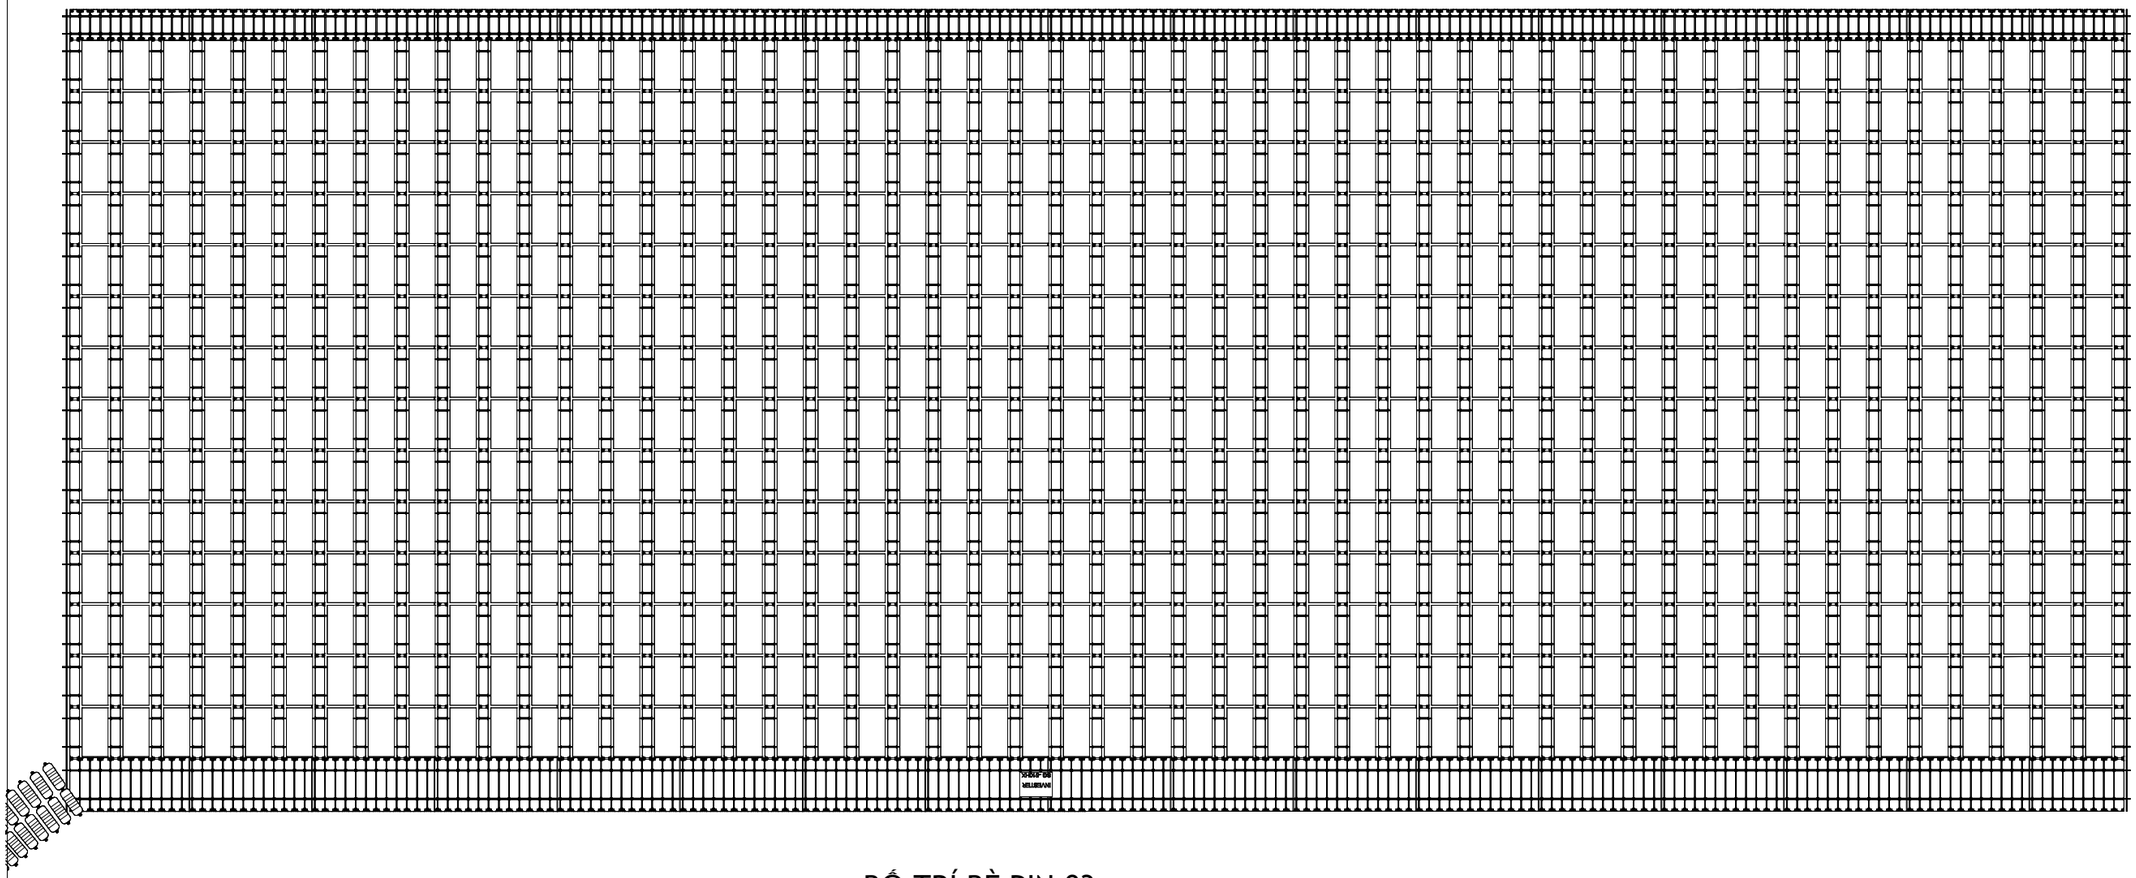

1 BỐ TRÍ BÈ PIN 03

1 : 300

SỐ PHAO NỔI THEO BÈ			
Family	DẢI PIN	SỐ LƯỢNG HÀNG	SỐ PHAO
Dải phao đi lại kèm đỡ invester	DẢI PHAO ĐI LẠI	1	201
Dai phaodi lai	DẢI PHAO ĐI LẠI	1	201
Dai phao do pin	DẢI PHAO ĐỠ PIN	51	714
Grand total: 53			1116

INVESTER		
Thiết bị	Loại Invester	Số lượng
Invester	SG -510HX	1
Grand total: 1		

THỐNG KÊ TẤM PIN MẶT TRỜI				
Cấu kiện	SỐ LƯỢNG HÀNG	Số tấm pin	Comments	So string
DẢI PIN MẶT TRỜI	50	700	be 5	25
Grand total: 50		700		25

SỬA REV.	NGÀY DATE	PHÊ DUYỆT APPRVD. BY	MÔ TẢ DESCRIPTION

N

DỰ ÁN / PROJECT:

CHỦ ĐẦU TƯ / INVESTOR:

TƯ VẤN QLDA & TVGS:

PHÊ DUYỆT/ APPROVED BY: | KÝ/ SIGN:

GIÁM SÁT THI CÔNG

NGƯỜI THỰC HIỆN: LÊ MINH NHẬT | KÝ/ SIGN:

HỒ SƠ / FILE:

HẠNG MỤC / ITEM: <None>

TÊN BẢN VẼ / DRAWING TITLE: Bố trí bè pin 3 Hồ Bản Mòng

TỶ LỆ / SCALE:	NGÀY / DATE:	HIỆU CHỈNH / REV.:
	.../2026	00

SỐ BẢN VẼ / DRAWING NO.: CT-BP-03

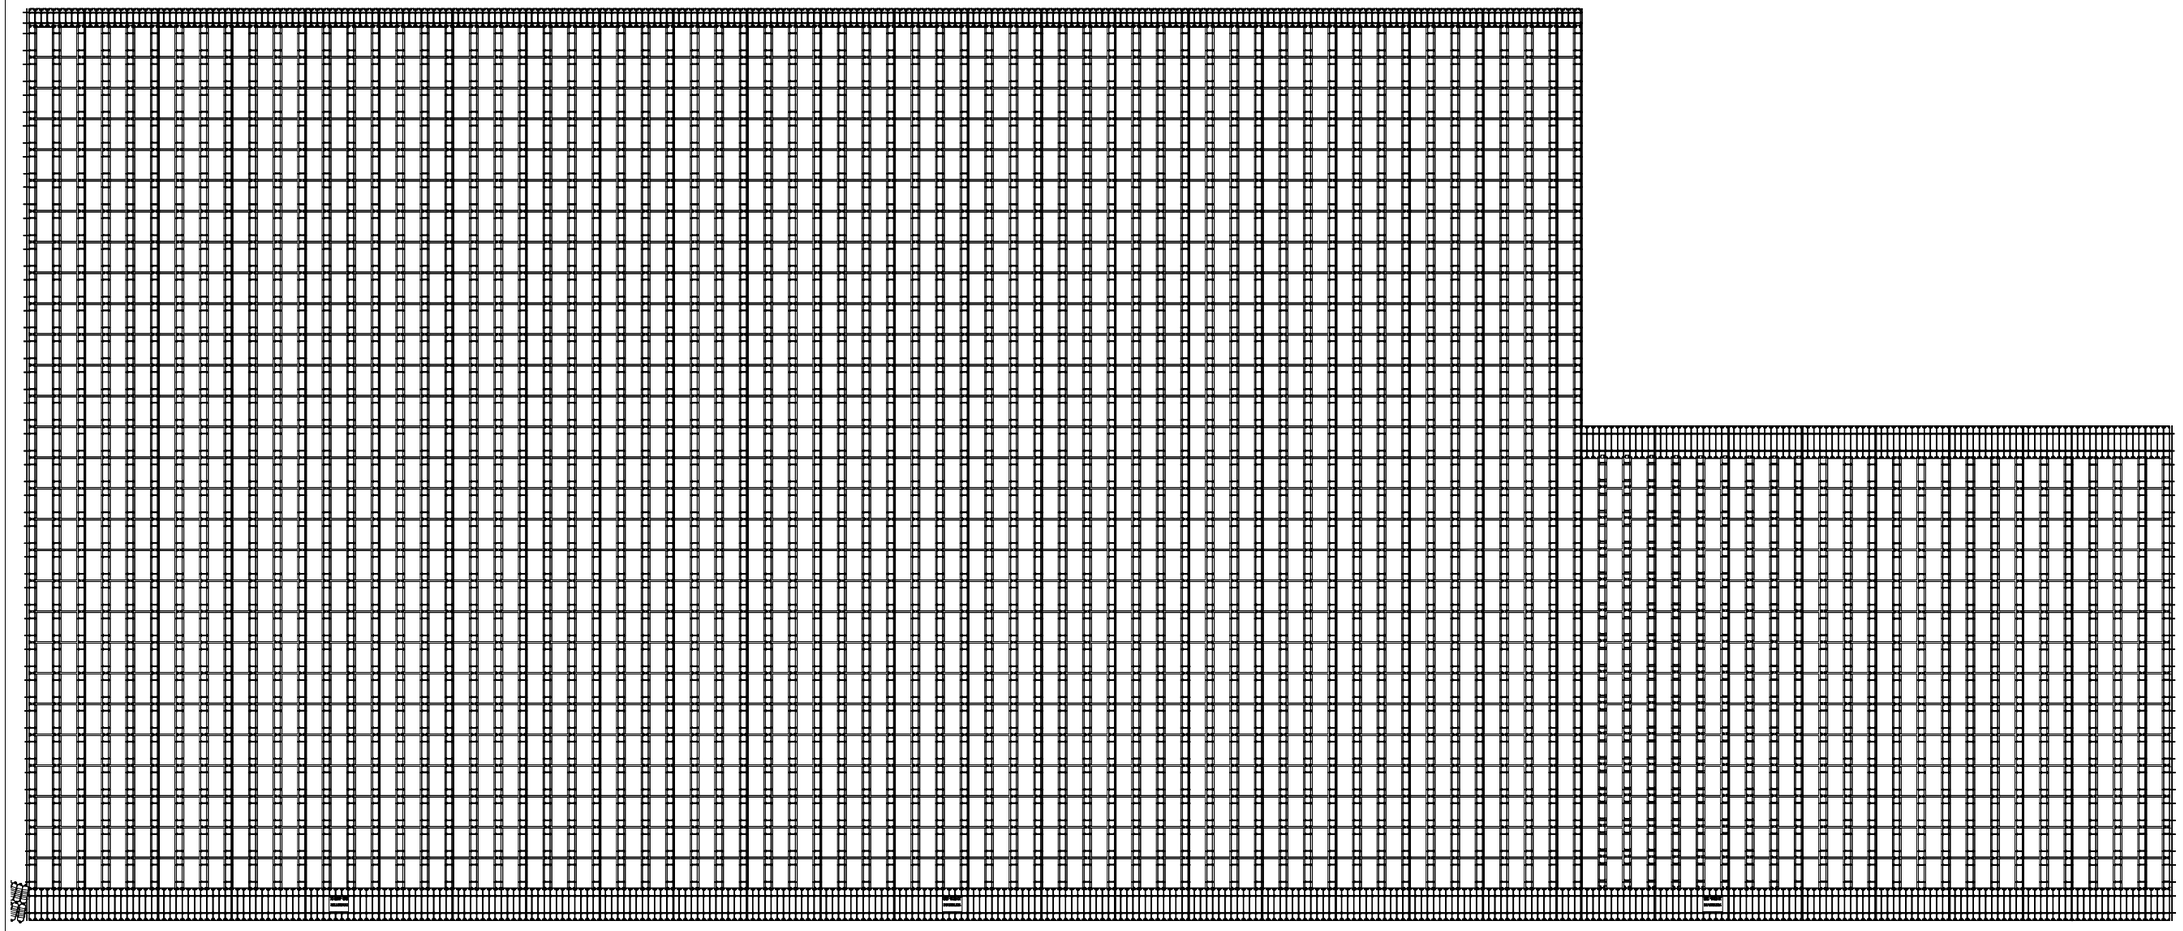

1 BỐ TRÍ BÈ PIN 04

1 : 500

SỐ PHAO NỔI THEO BÈ			
Family	DẢI PIN	SỐ LƯỢNG HÀNG	SỐ PHAO
Dai phaodi lai	DẢI PHAO ĐI LẠI	1	253
Dải phao đi lại kèm đỡ invester	DẢI PHAO ĐI LẠI	2	445
Dai phao do pin	DẢI PHAO ĐỠ PIN	88	2128
Grand total: 91			2826

INVESTER		
Thiết bị	Loại Invester	Số lượng
Invester	SG -510HX	3
Grand total: 3		

THỐNG KÊ TẤM PIN MẶT TRỜI				
Cấu kiện	SỐ LƯỢNG HÀNG	Số tấm pin	Comments	So string
DẢI PIN MẶT TRỜI	87	2100	be 4	75
Grand total: 87		2100		75

SỬA REV.	NGÀY DATE	PHÊ DUYỆT APPRVD. BY	MÔ TẢ DESCRIPTION

N

DỰ ÁN / PROJECT:

CHỦ ĐẦU TƯ / INVESTOR:

TƯ VẤN QLDA & TVGS:

PHÊ DUYỆT/ APPROVED BY: | KÝ/ SIGN:

GIÁM SÁT THI CÔNG

NGƯỜI THỰC HIỆN: LÊ MINH NHẬT | KÝ/ SIGN:

HỒ SƠ / FILE:

HẠNG MỤC / ITEM: <None>

TÊN BẢN VẼ / DRAWING TITLE: Bố trí bè pin 4 Hồ Bản Mòng

TỶ LỆ / SCALE:	NGÀY / DATE:	HIỆU CHỈNH / REV.:
	.../2026	00

SỐ BẢN VẼ / DRAWING NO.: CT-BP-04

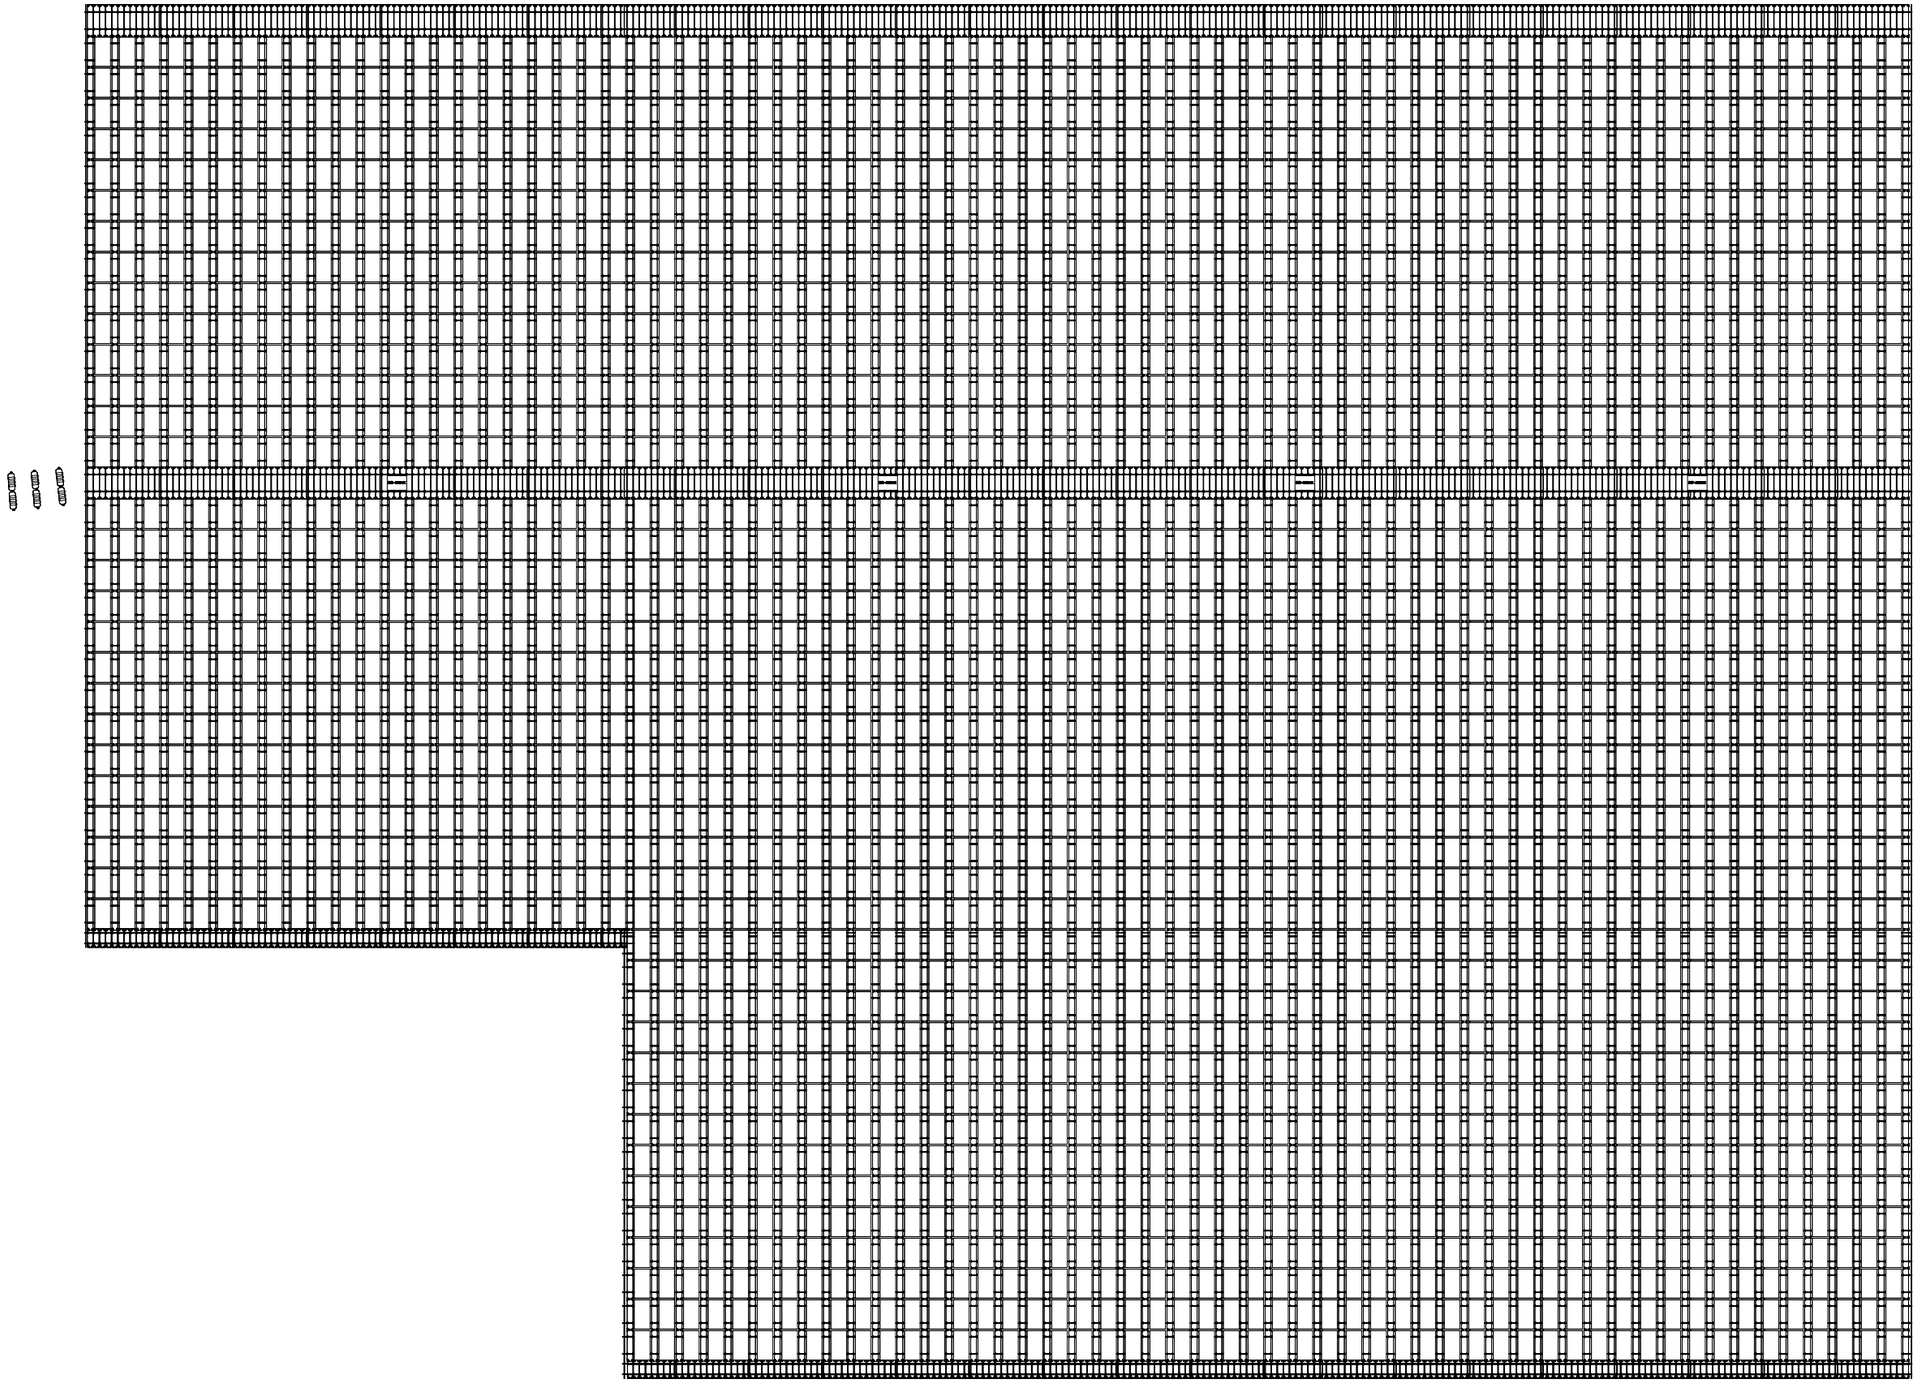

1 BỐ TRÍ BÈ PIN 05

1 : 500

INVESTER		
Thiết bị	**Loại Invester**	**Số lượng**
Invester	SG -510HX	4
Grand total: 4		

THỐNG KÊ TẤM PIN MẶT TRỜI				
Cấu kiện	**SỐ LƯỢNG HÀNG**	**Số tấm pin**	**Comments**	**So string**
DẢI PIN MẶT TRỜI	148	2800	be 6	100
Grand total: 148		2800		100

SỐ PHAO NỔI THEO BÈ			
Family	**DẢI PIN**	**SỐ LƯỢNG HÀNG**	**SỐ PHAO**
Dải phao đi lại kèm đỡ invester	DẢI PHAO ĐI LẠI	2	594
Dai phaodi lai	DẢI PHAO ĐI LẠI	2	297
Dai phao do pin	DẢI PHAO ĐỠ PIN	150	2842
Grand total: 154			3733

SỬA REV.	NGÀY DATE	PHÊ DUYỆT APPRVD. BY	MÔ TẢ DESCRIPTION

N

DỰ ÁN / PROJECT:

CHỦ ĐẦU TƯ / INVESTOR:

TƯ VẤN QLDA & TVGS:

PHÊ DUYỆT/ APPROVED BY: | KÝ/ SIGN:

GIÁM SÁT THI CÔNG

NGƯỜI THỰC HIỆN: LÊ MINH NHẬT | KÝ/ SIGN:

HỒ SƠ / FILE:

HẠNG MỤC / ITEM: <None>

TÊN BẢN VẼ / DRAWING TITLE: SƠ PHAO pin 5 Hồ Bản Mòng

TỶ LỆ / SCALE:	NGÀY / DATE:	HIỆU CHỈNH / REV.:
	.../2026	00

SỐ BẢN VẼ / DRAWING NO.: CT-BP-05

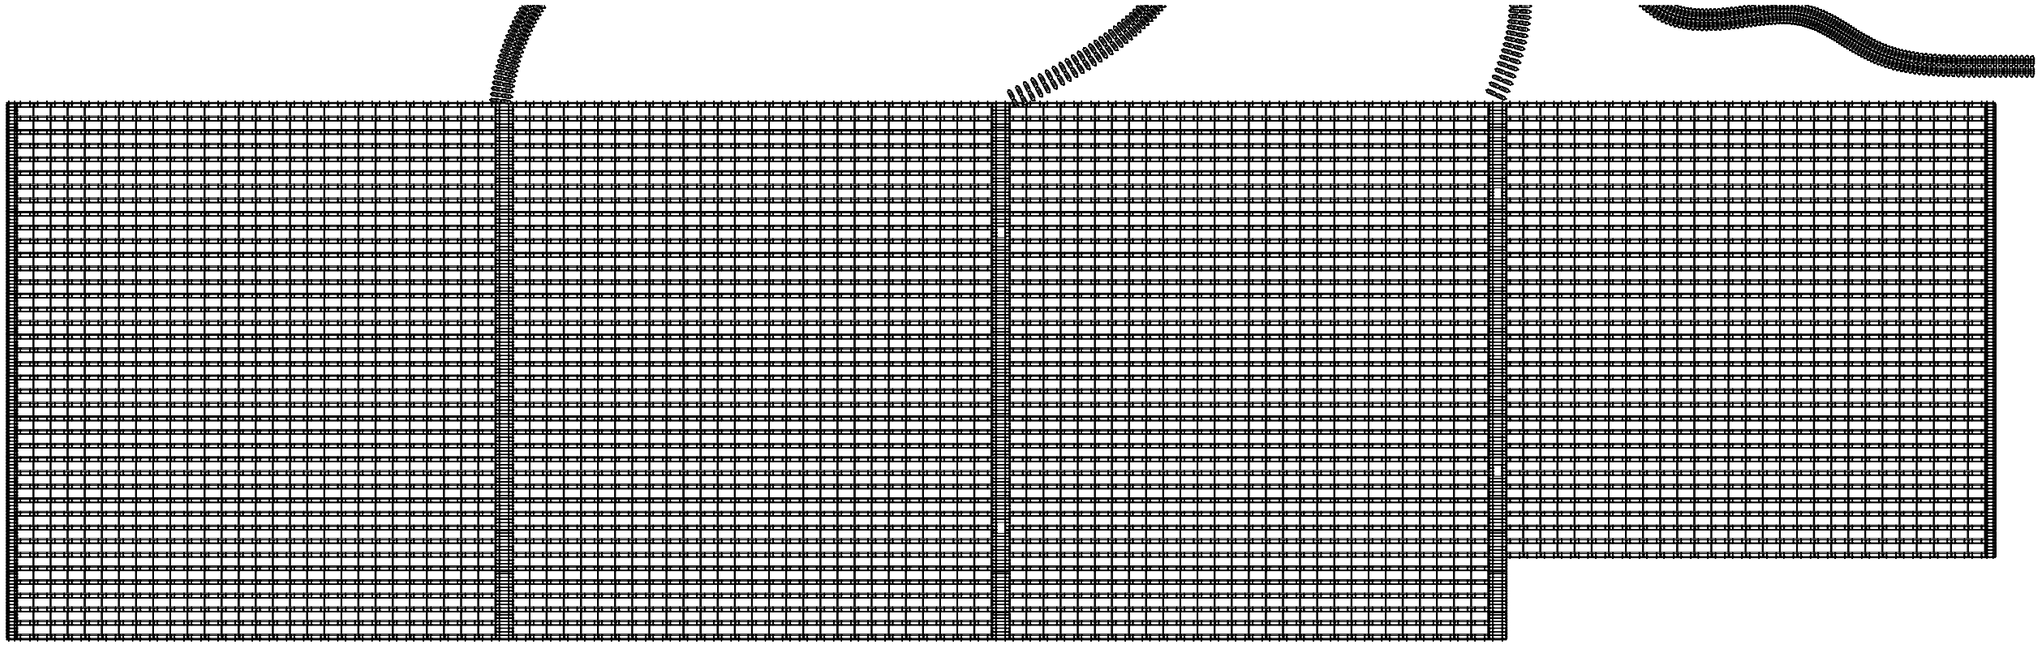

1 BỐ TRÍ BÈ PIN 06

1 : 900

INVESTER		
Thiết bị	**Loại Invester**	**Số lượng**
Invester	SG -510HX	4
Grand total: 4		

THỐNG KÊ TẤM PIN MẶT TRỜI				
Cấu kiện	**SỐ LƯỢNG HÀNG**	**Số tấm pin**	**Comments**	**So string**
DẢI PIN MẶT TRỜI	150	4200	be 7	150
Grand total: 150		4200		150

SỐ PHAO NỔI THEO BÈ			
Family	**DẢI PIN**	**SỐ LƯỢNG HÀNG**	SỐ PHAO
Dai phaodi lai	DẢI PHAO ĐI LẠI	2	290
Dải phao đi lại kèm đỡ invester	DẢI PHAO ĐI LẠI	3	471
Dai phao do pin	DẢI PHAO ĐỠ PIN	154	4312
Grand total: 159			5073

SỬA REV.	NGÀY DATE	PHÊ DUYỆT APPRVD. BY	MÔ TẢ DESCRIPTION

N

DỰ ÁN / PROJECT:

CHỦ ĐẦU TƯ / INVESTOR:

TƯ VẤN QLDA & TVGS:

PHÊ DUYỆT/ APPROVED BY: | KÝ/ SIGN:

GIÁM SÁT THI CÔNG

NGƯỜI THỰC HIỆN: LÊ MINH NHẬT | KÝ/ SIGN:

HỒ SƠ / FILE:

HẠNG MỤC / ITEM: <None>

TÊN BẢN VẼ / DRAWING TITLE: Bố trí bè pin 6 Hồ Bản Mòng

TỶ LỆ / SCALE:	NGÀY / DATE:	HIỆU CHỈNH / REV.:
	.../2026	00

SỐ BẢN VẼ / DRAWING NO.: CT-BP-06